


נעילה

Stainless Steel finish

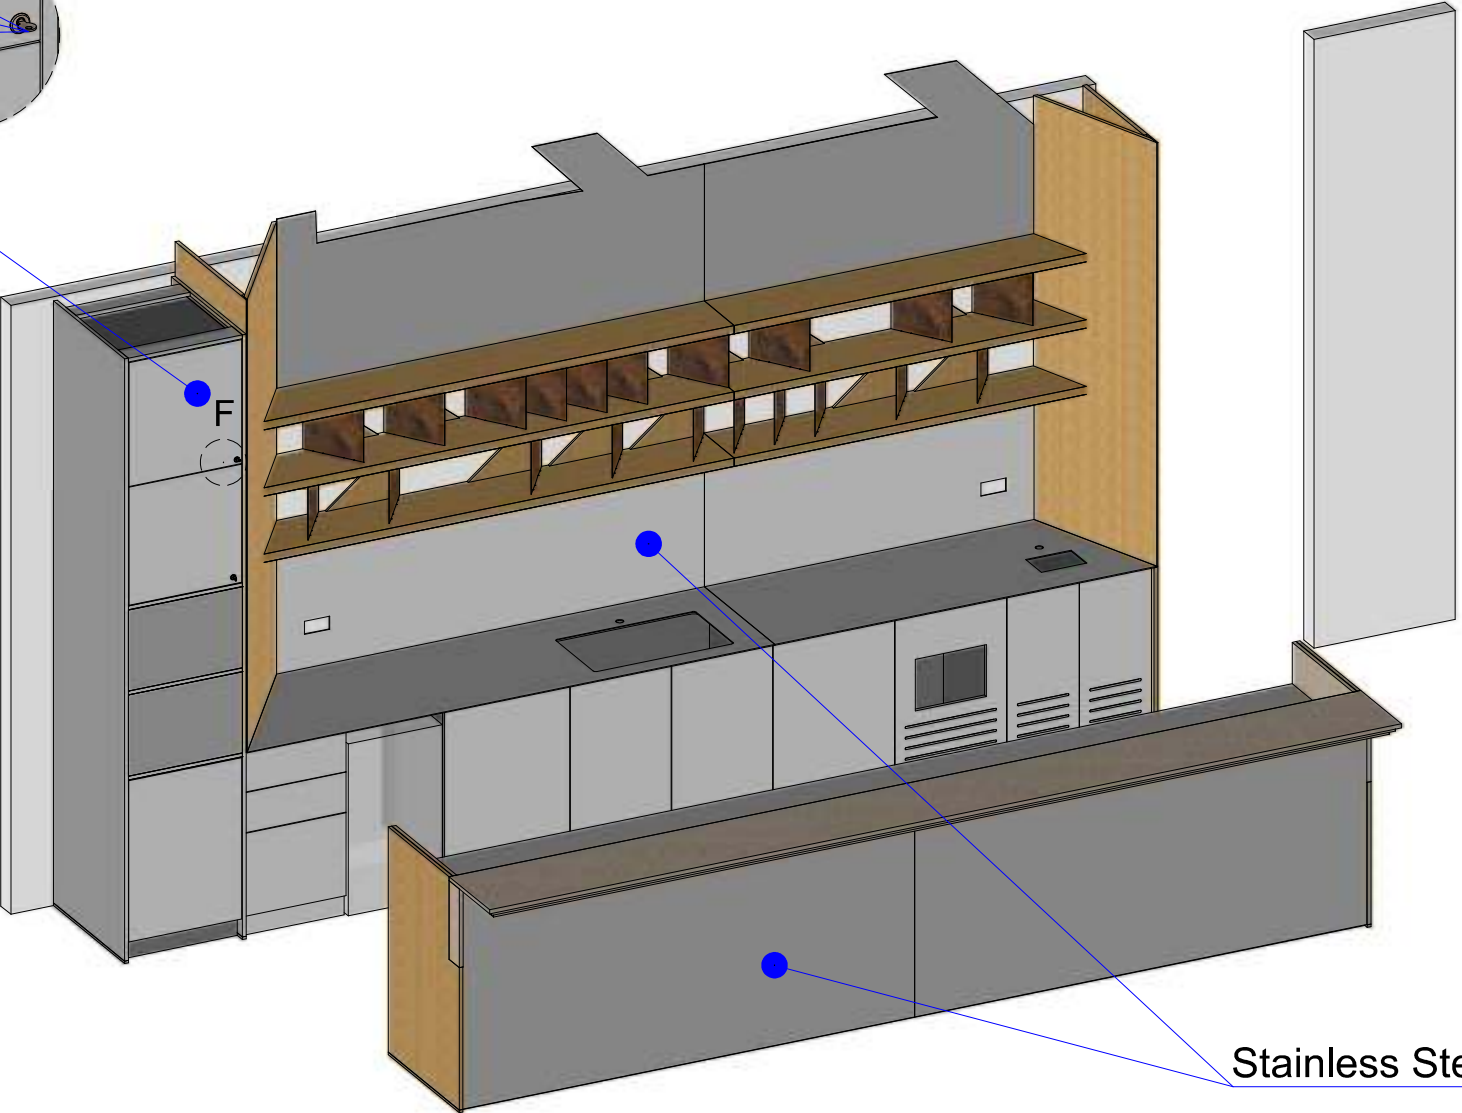


Stainless Steel

- מטבח ראשי ובר כולל שיש | RA-N01
- 1: Kitchen-Front
- 1.1: Exterior: Metal-Stainless Steel by sample • Missing: Supplier
 - 1.2: Interior: Formica Birman, 2650
 - 1.3: Handles: qty? Domicile, 0583T.70.13
 - 1.4: Toe kick: Metal-Stainless Steel by sample • Missing: Supplier
 - 1.5: Countertop: Metal-Stainless Steel by sample • Missing: Supplier
 - 1.6: Backsplash: Metal-Stainless Steel by sample • Missing: Supplier
- 2: Kitchen-Island
- 2.1: Exterior: Metal-Stainless Steel by sample • Missing: Supplier
 - 2.2: Interior: Formica Birman, 2650
 - 2.3: Handles: qty? Domicile, 0583T.70.13
 - 2.4: Toe kick: Metal-Stainless Steel by sample • Missing: Supplier
 - 2.5: Countertop: Stone Marble, Laba Rosa
 - 2.6: Backsplash: Stone Marble, Laba Rosa
- 3: Shelf
- 3.1: Exterior: Veneer-Oak NextDoor, DOLY by sample
 - 3.2: Partitions-A: Veneer-Oak NextDoor, DOLY by sample
 - 3.3: Partitions-B: Metal-Corten by sample • Missing: Supplier


Material	Sumilation	Real
Veneer-Oak - NextDoor, DOLY		
Corten		
Stainless Steel		
Stone Marble, Laba Rosa		Stone Marble, Laba Rosa
Formica Birman, 2650		

Author:	Abdallah	Rooms Asolelim Fr 5 P464+294	Project name	NEXTDOOR
Date:	16/02/2026	מטבח ראשי ובר כולל שיש RA-N01	Part Room Place	
# 7/17	Scale: 1:10	RA-N01	File name	
				טל-03-602-3004

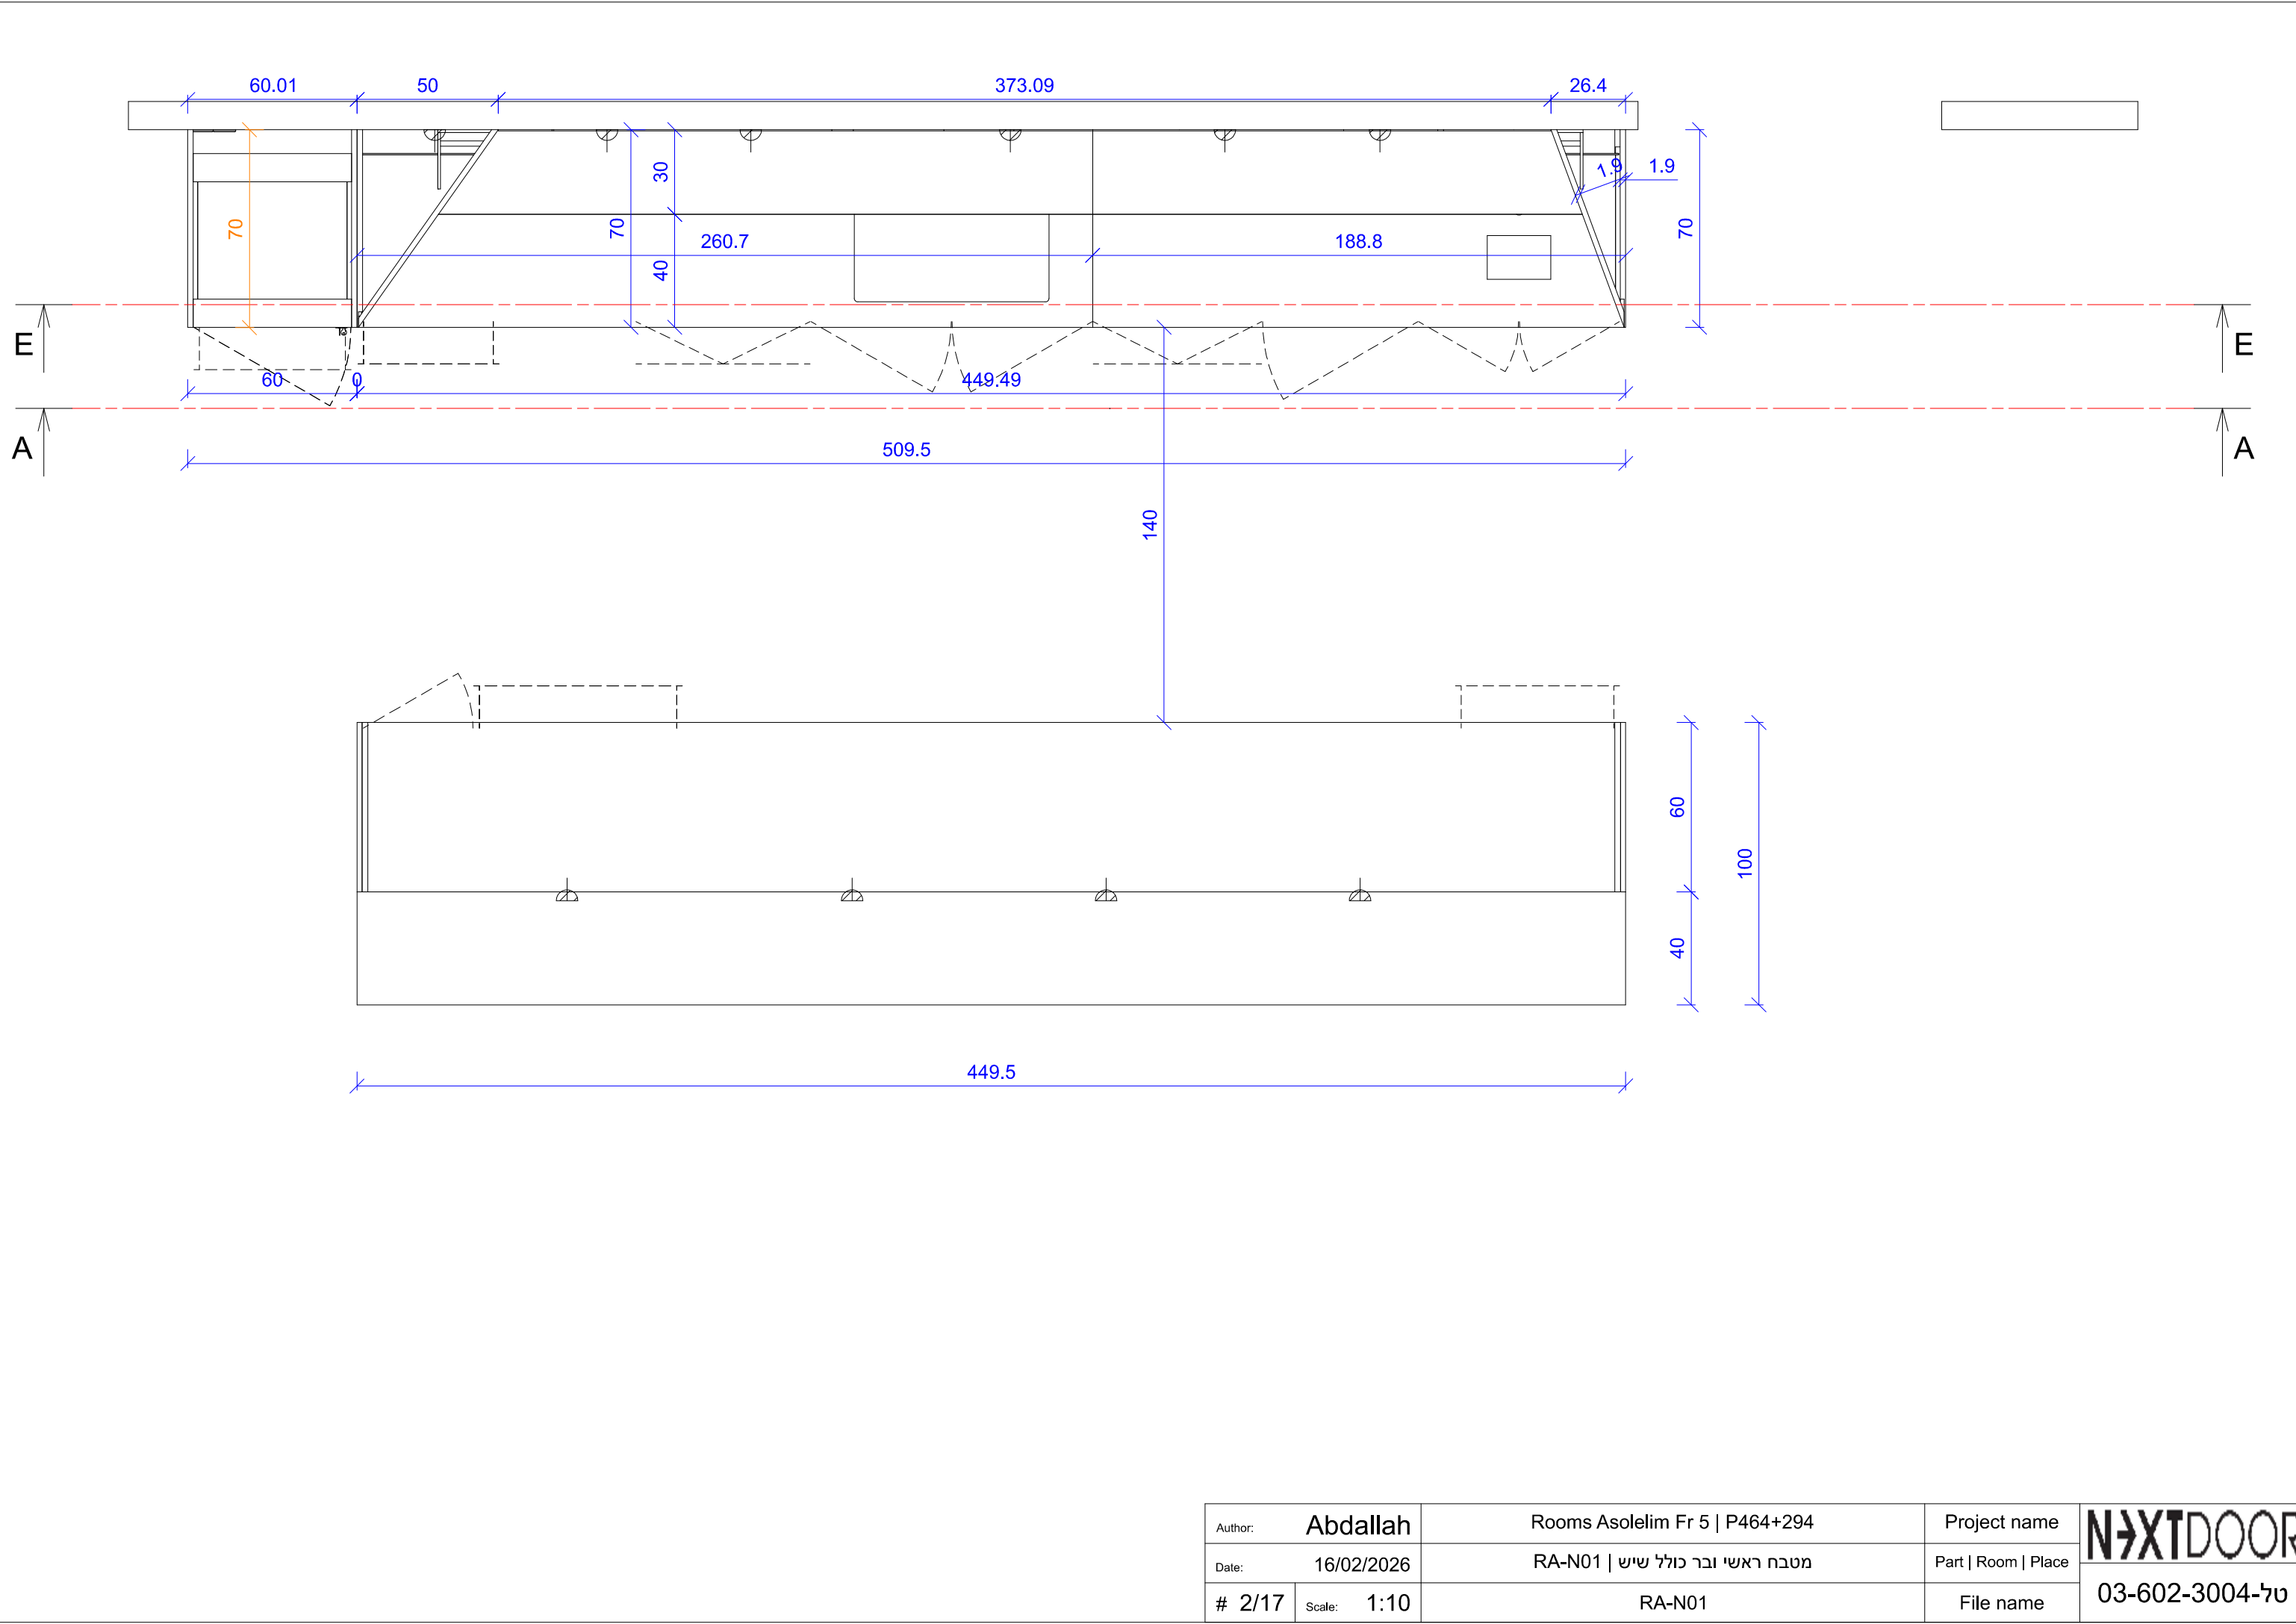


Author:	Abdallah	Rooms Asolelim Fr 5 P464+294	Project name	NXTDOOR
Date:	16/02/2026	מטבח ראשי ובר כולל שיש RA-N01	Part Room Place	
# 2/17	Scale: 1:10	RA-N01	File name	


טל-03-602-3004

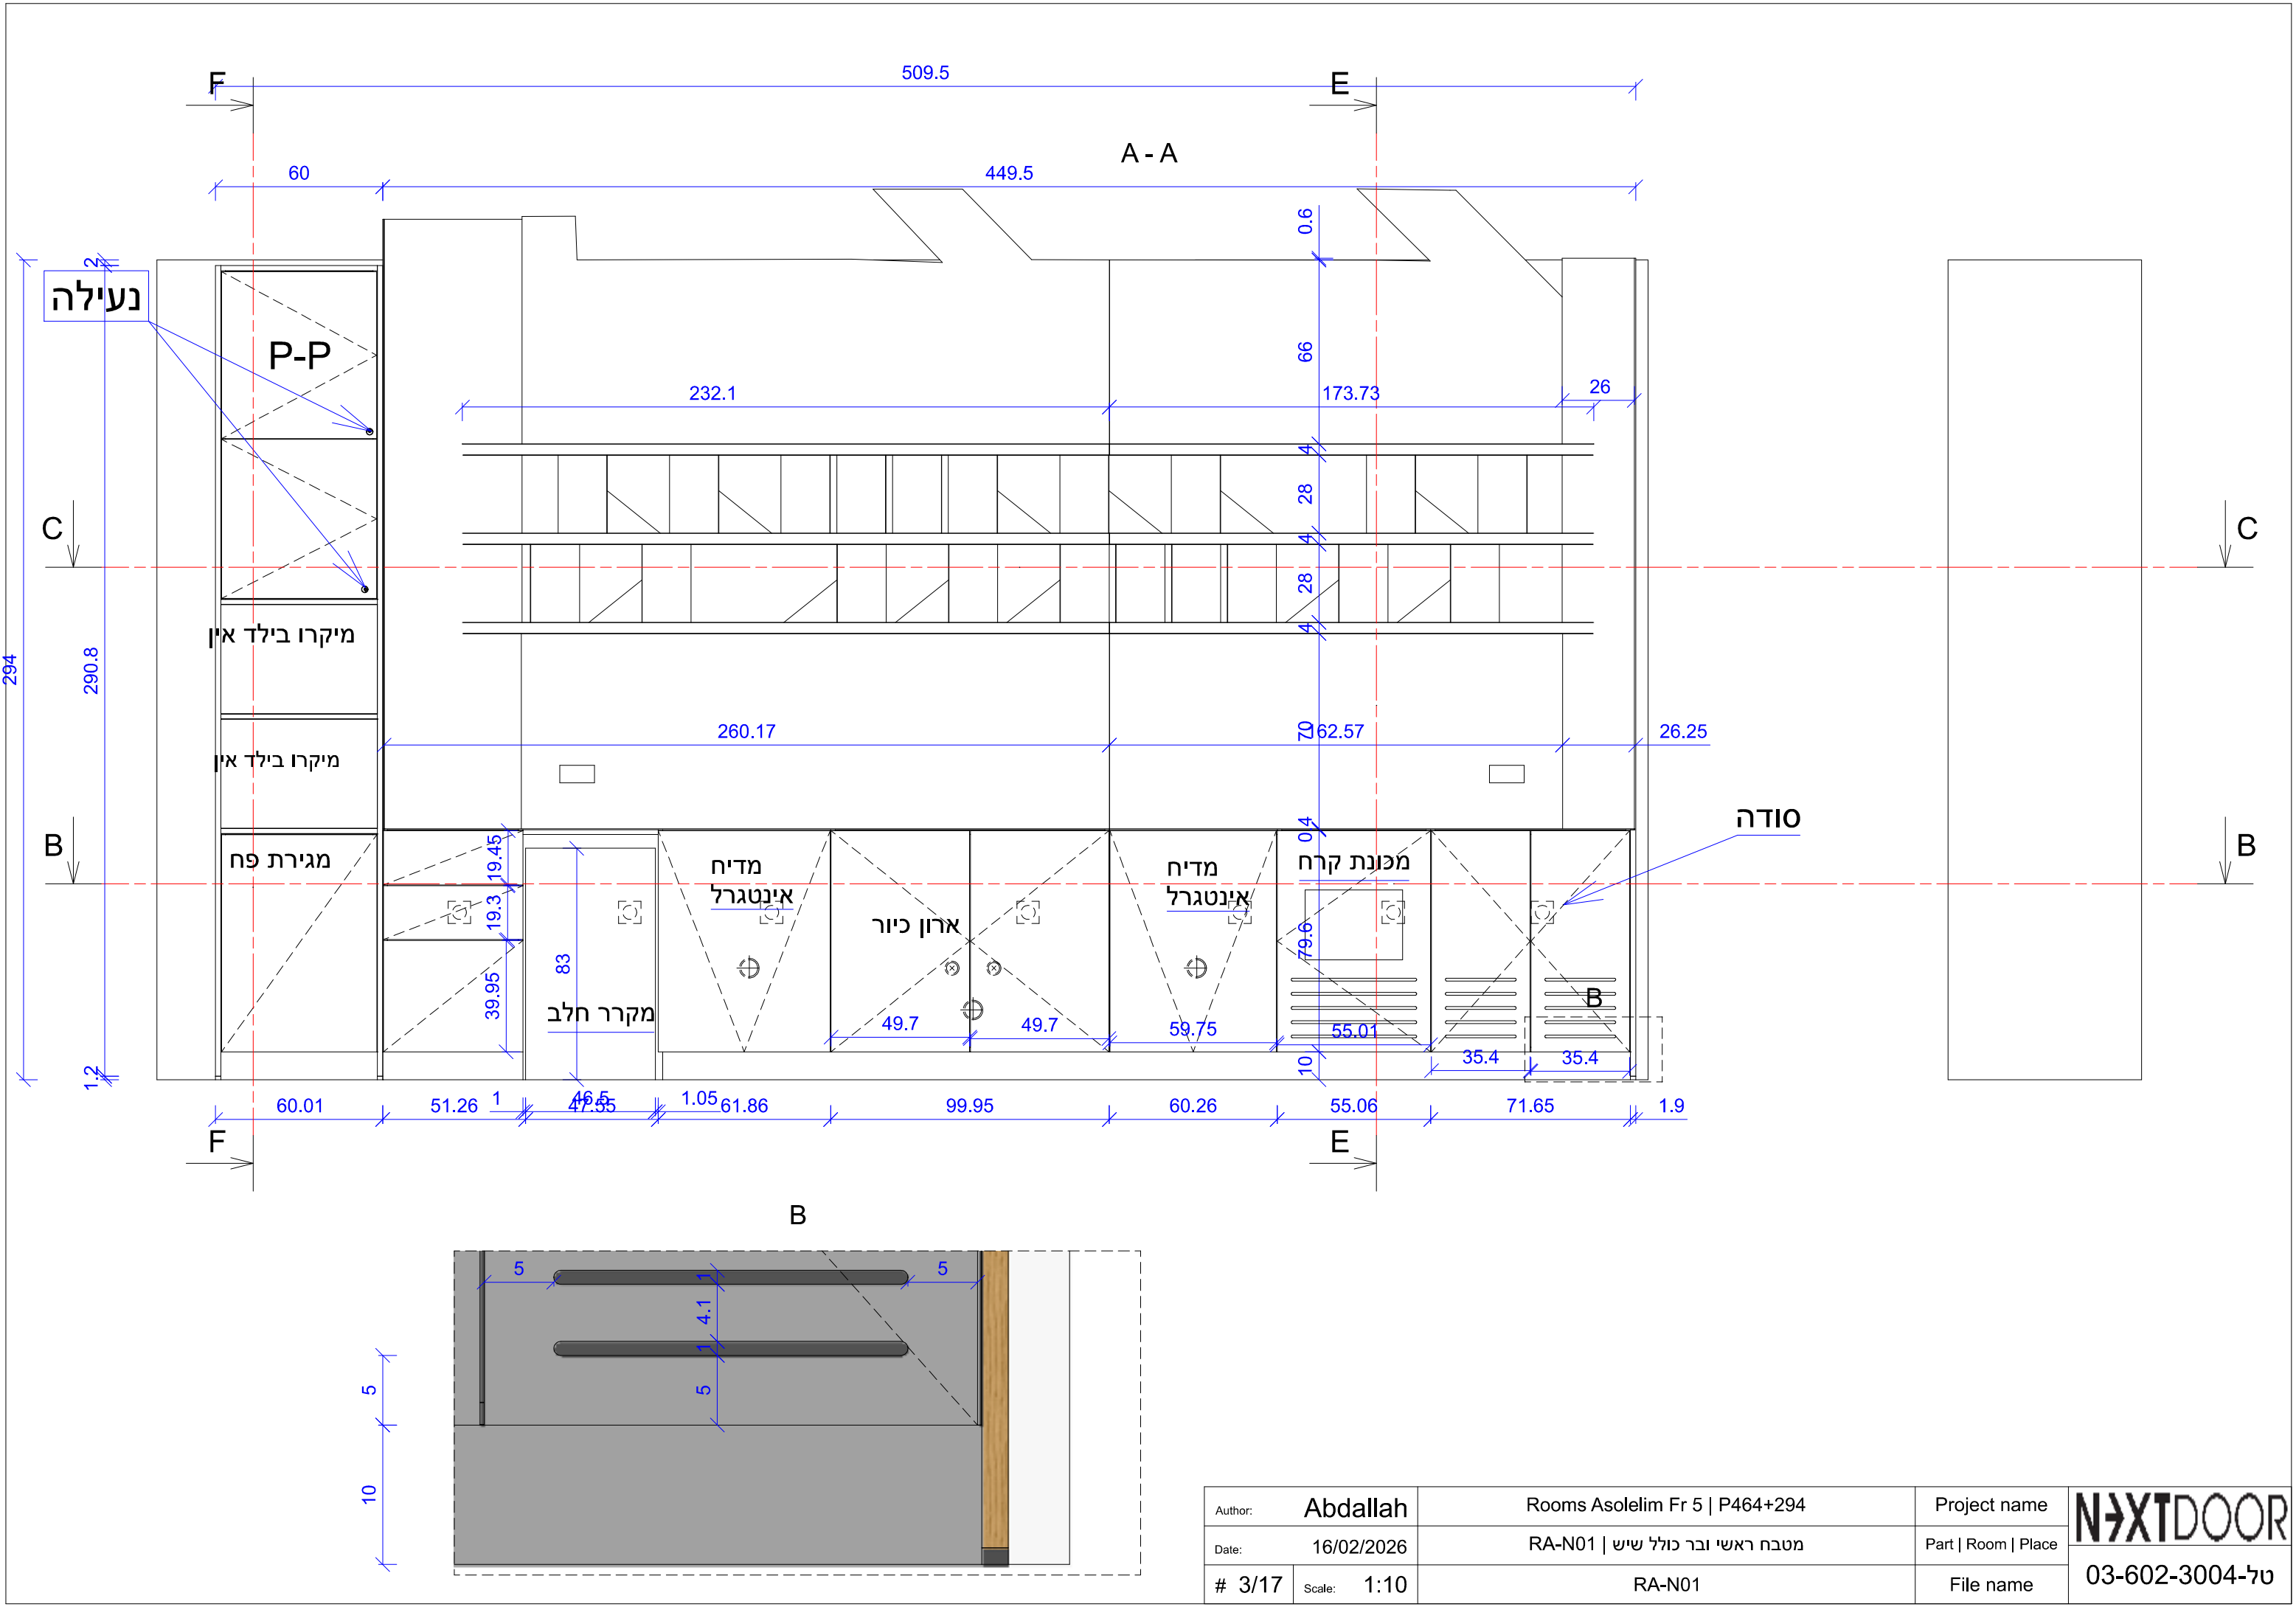



Author: Abdallah		Rooms Asolelim Fr 5 P464+294	Project name	NEXTDOOR טל-03-602-3004
Date: 16/02/2026		מטבח ראשי ובר כולל שיש RA-N01	Part Room Place	
# 3/17	Scale: 1:10	RA-N01	File name	

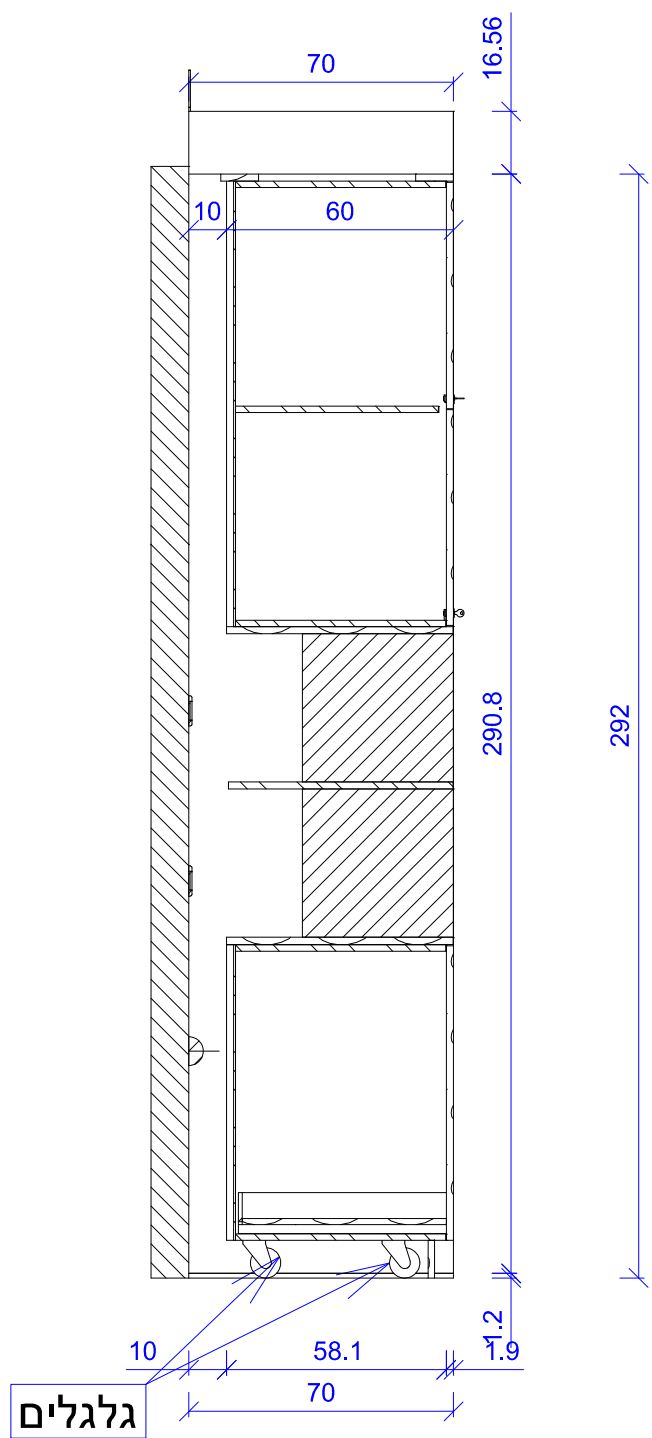


F - F

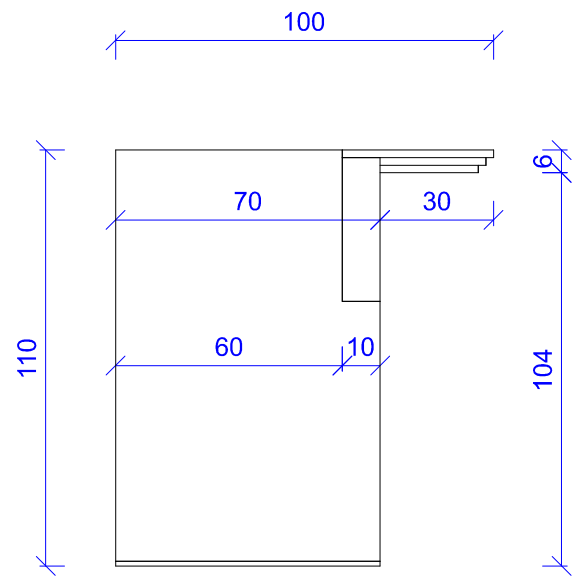



E - E

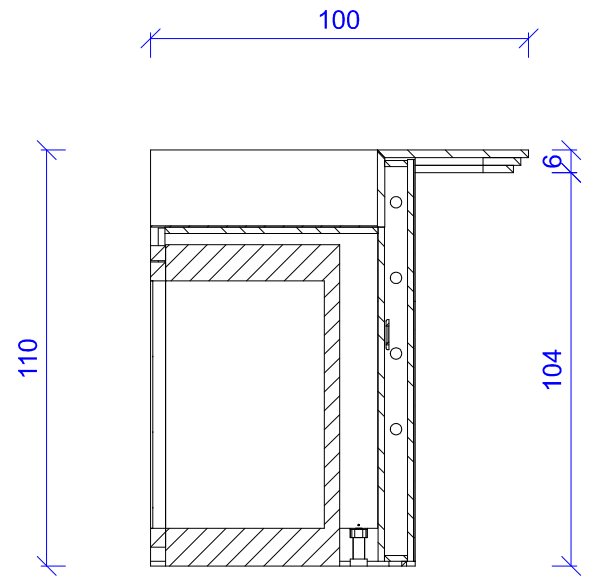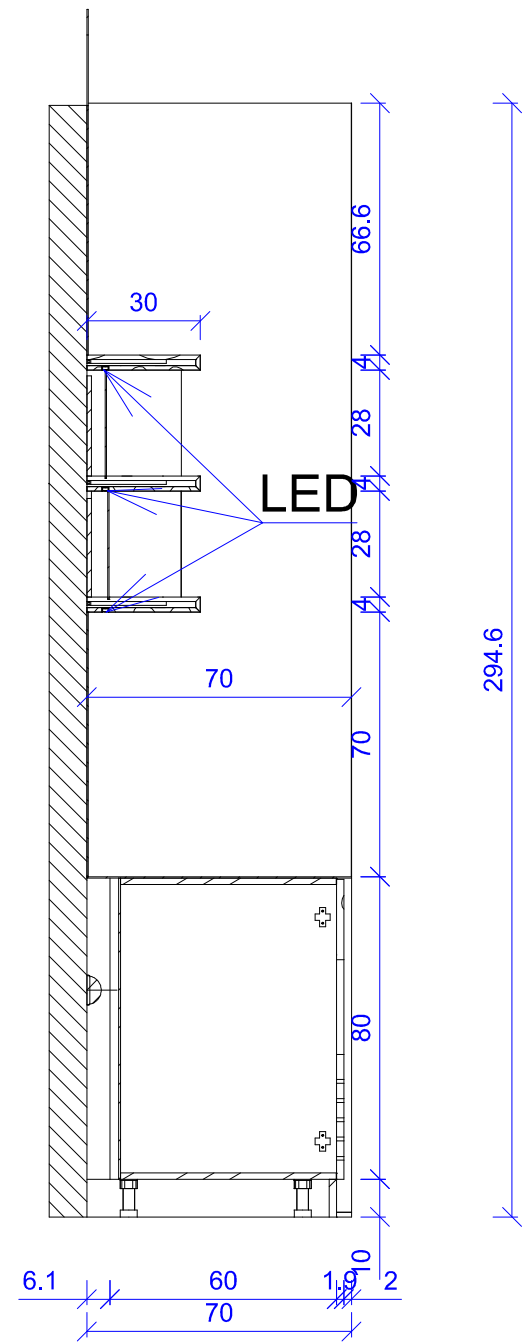







Author:	Abdallah	Rooms Asolelim Fr 5 P464+294	Project name	NXTDOOR טל-03-602-3004
Date:	16/02/2026	מטבח ראשי ובר כולל שיש RA-N01	Part Room Place	
# 6/17	Scale: 1:10	RA-N01	File name	

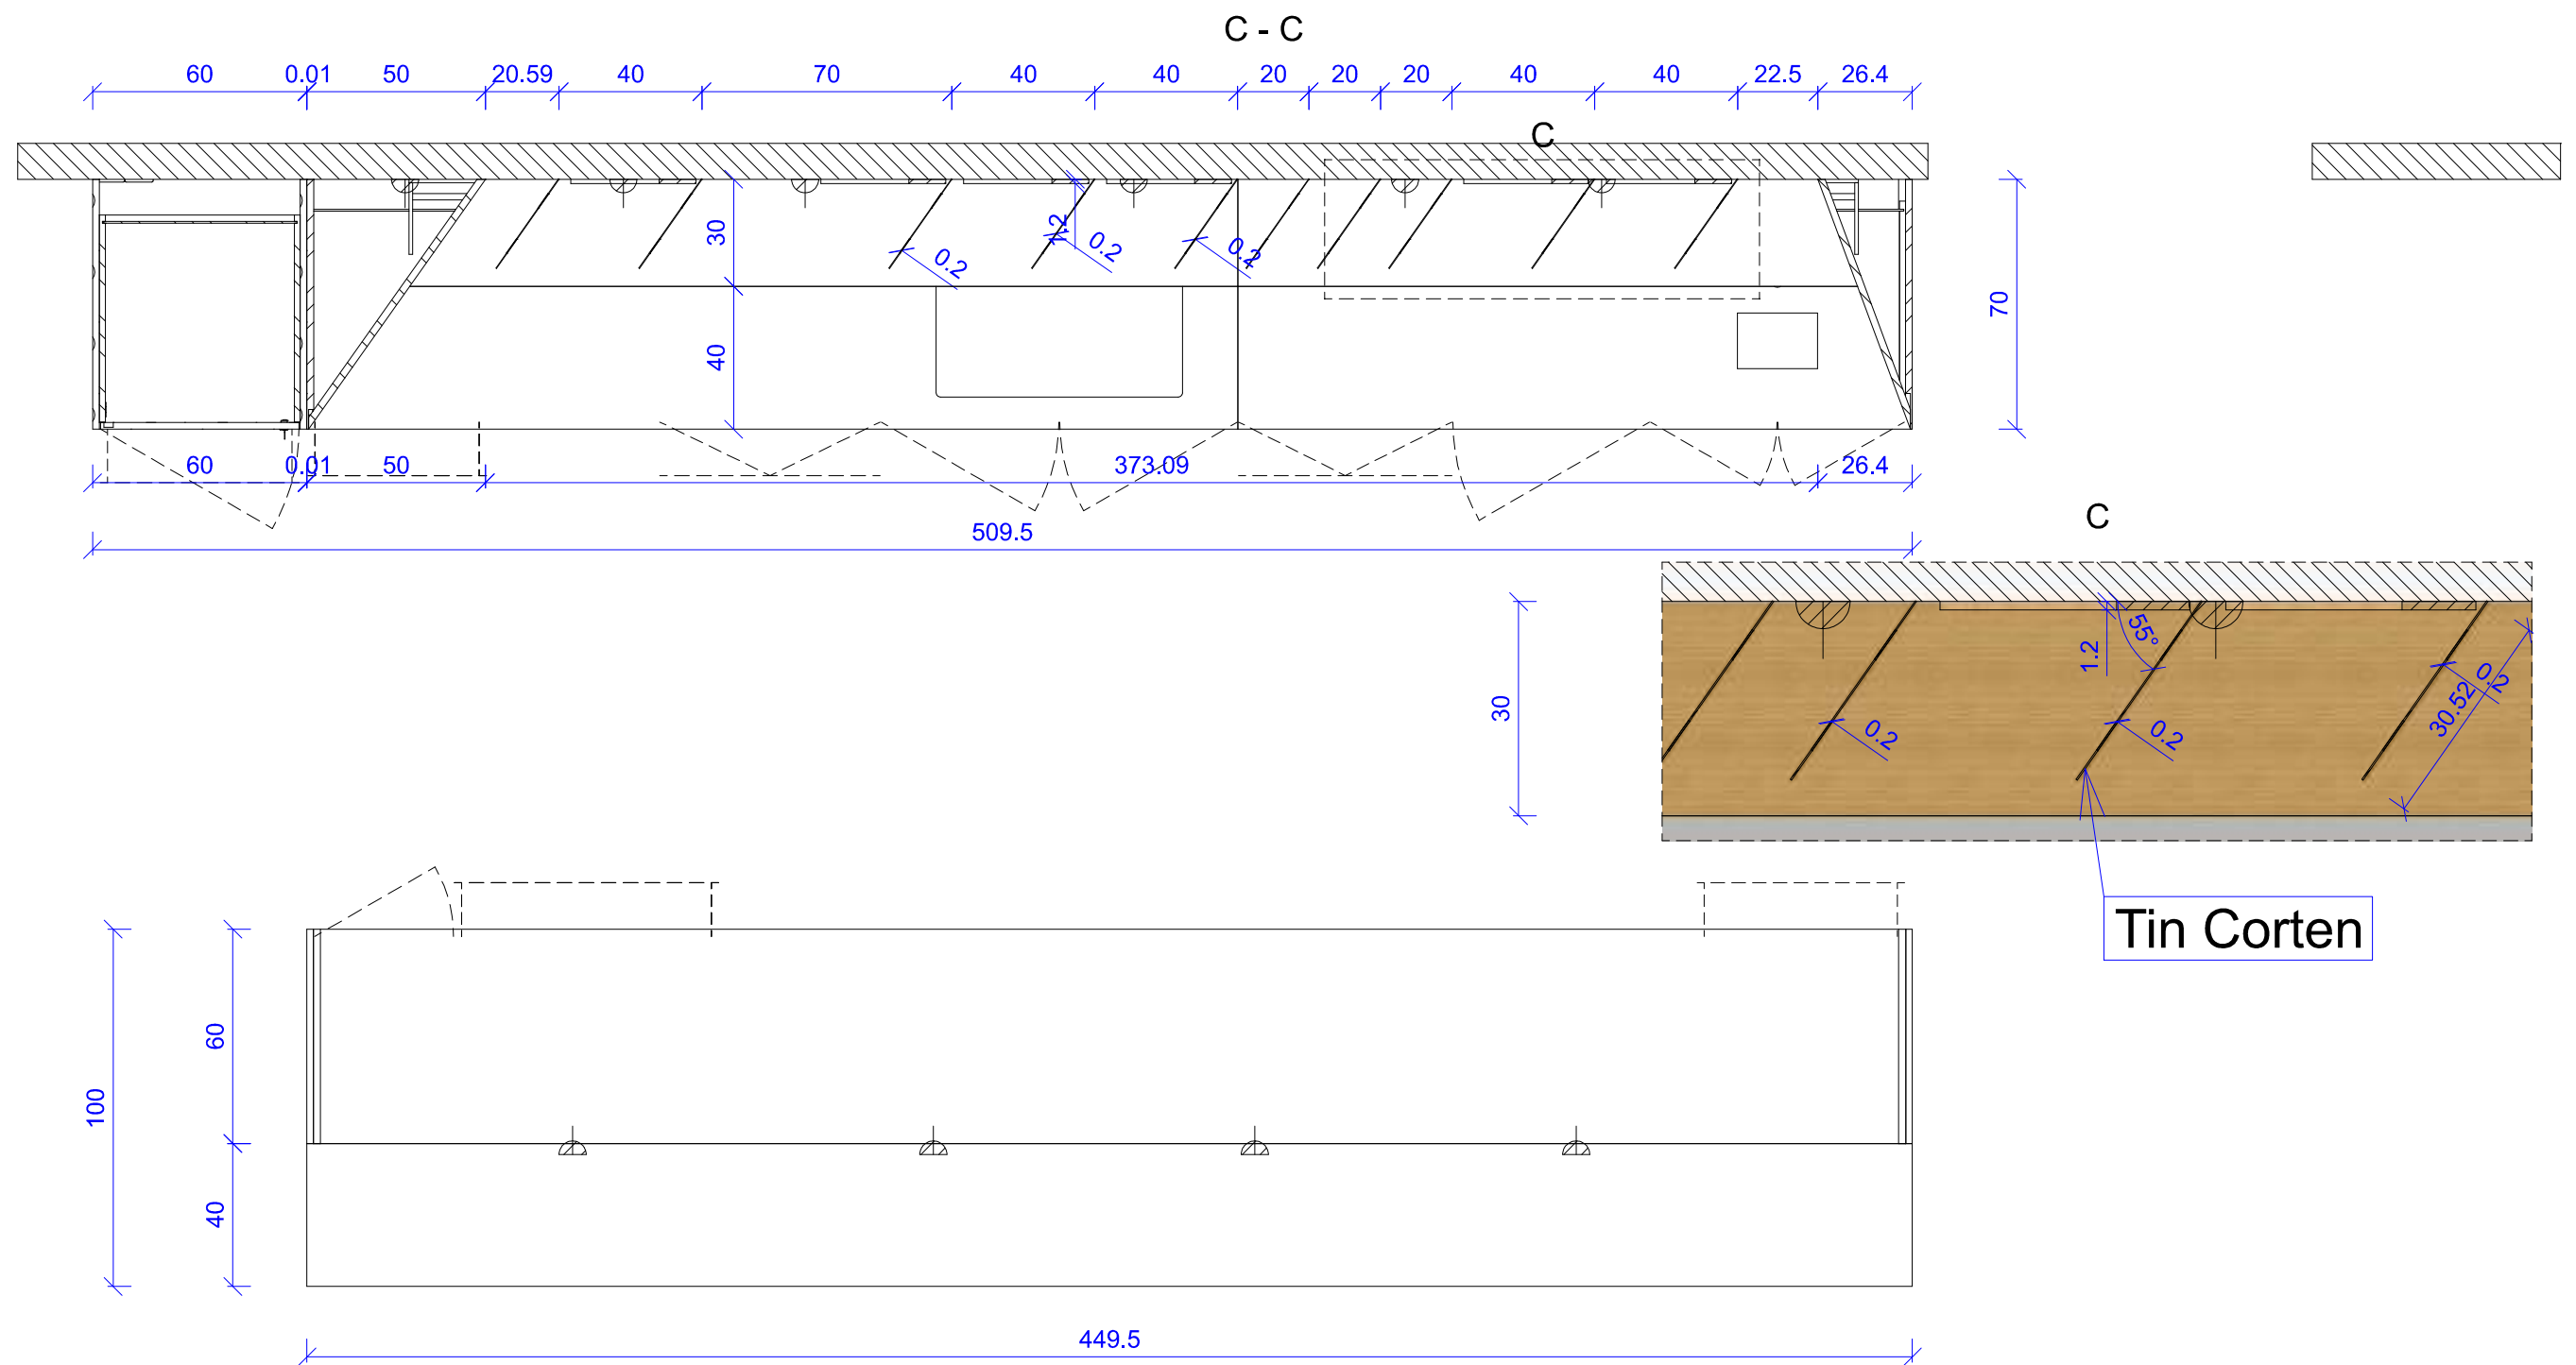


Author: Abdallah		Rooms Asolelim Fr 5 P464+294	Project name	N→XTDOOR
Date: 16/02/2026		מטבח ראשי ובר כולל שיש RA-N01	Part Room Place	
# 9/17	Scale: 1:10	RA-N01	File name	

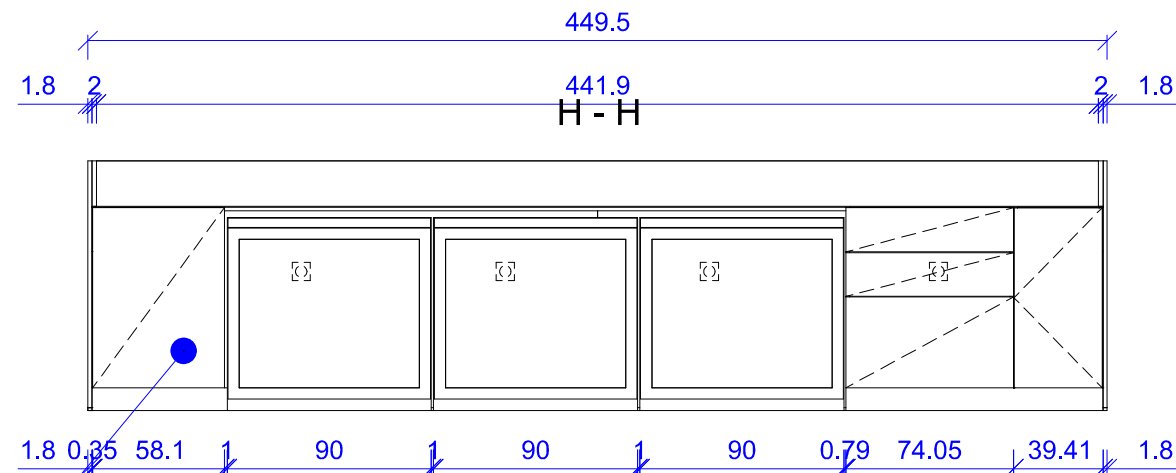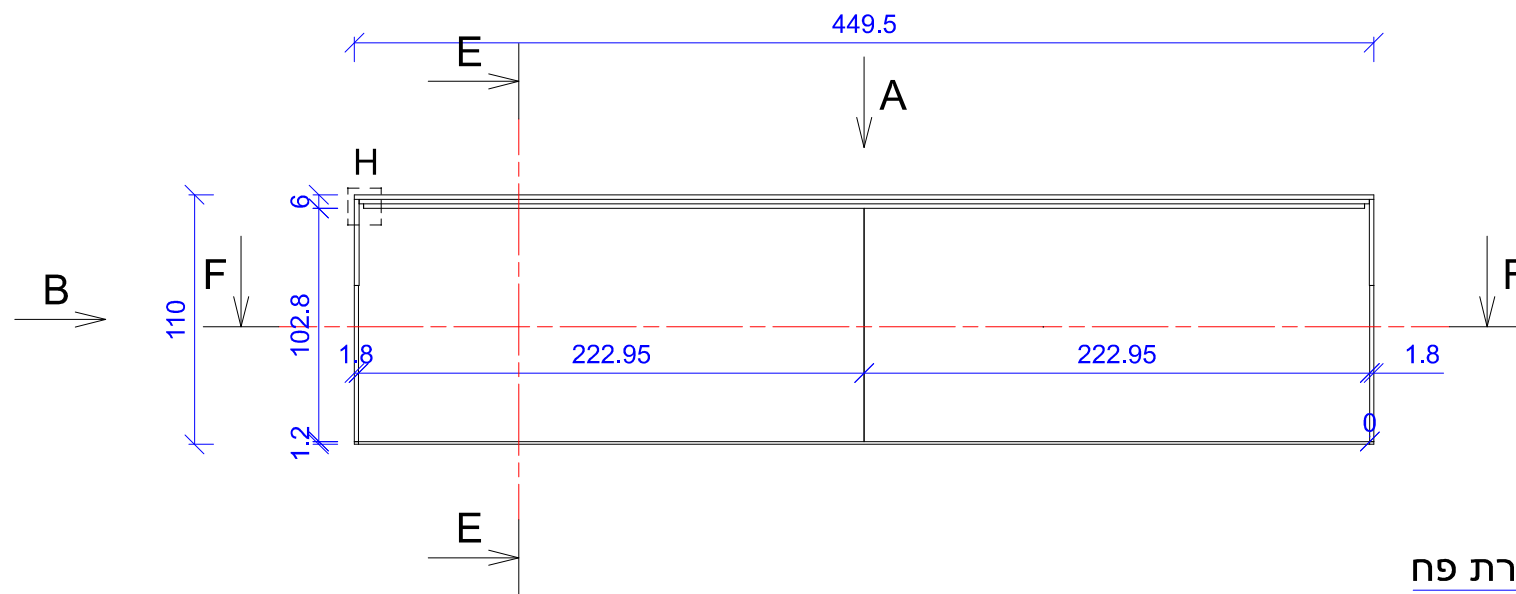

מגירת פח

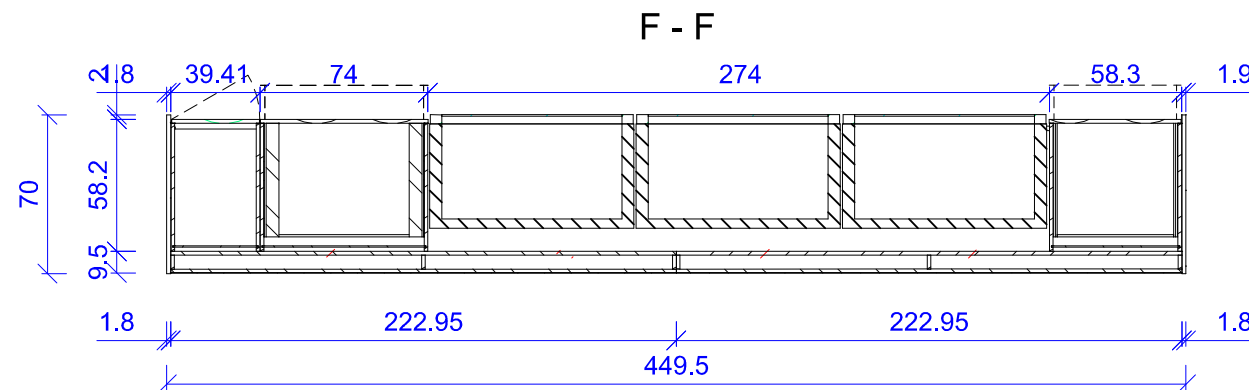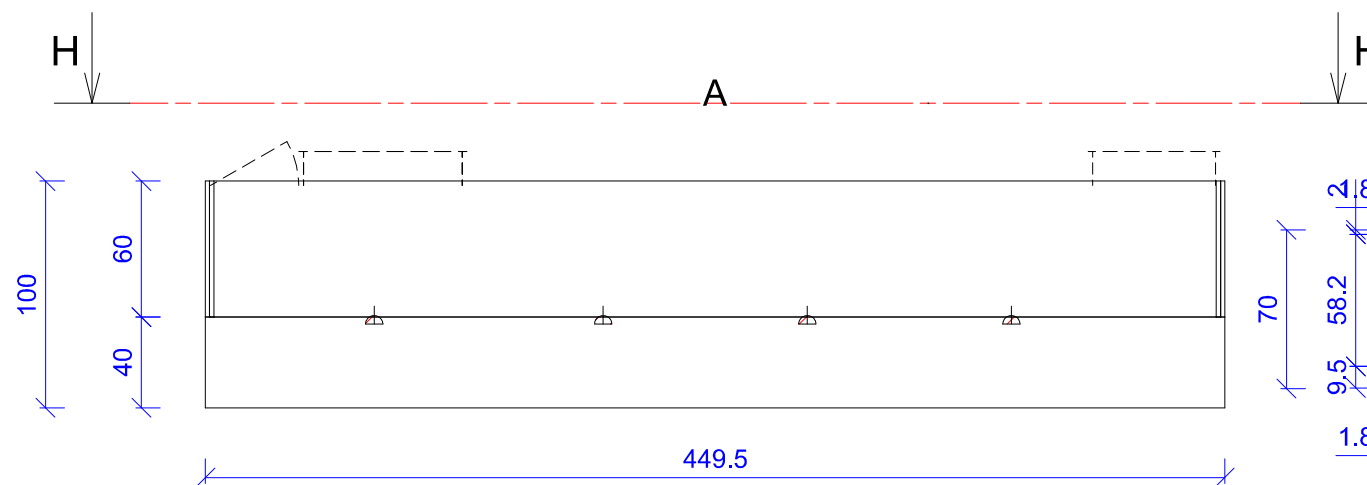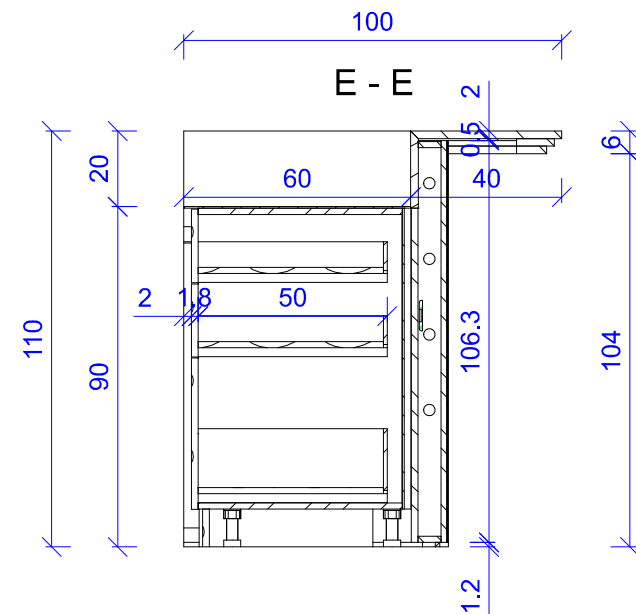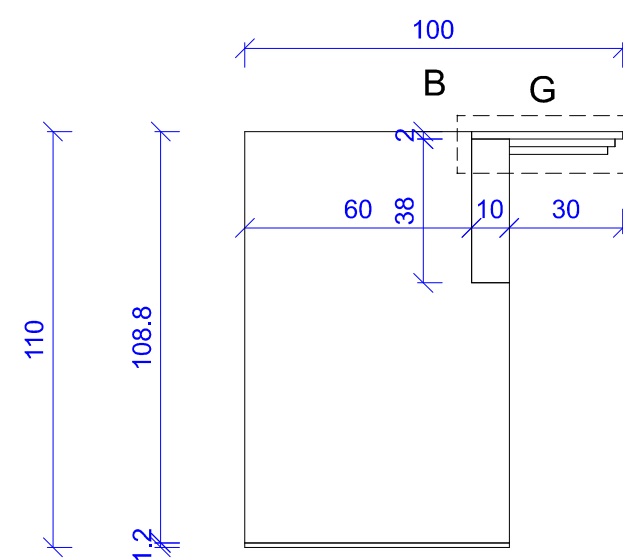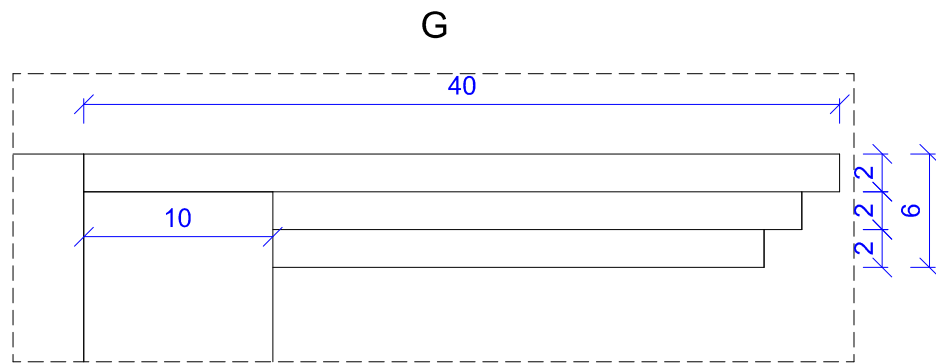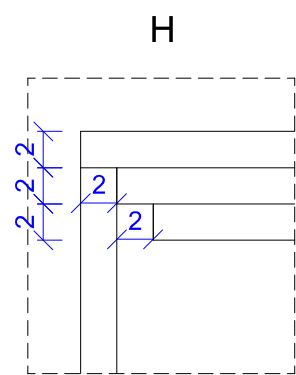


Author: Abdallah		Rooms Asolelim Fr 5 P464+294	Project name	N→XTDOOR
Date: 16/02/2026		מטבח ראשי ובר כולל שיש RA-N01	Part Room Place	
#10/17	Scale: 1:10	RA-N01	File name	
				טל-03-602-3004

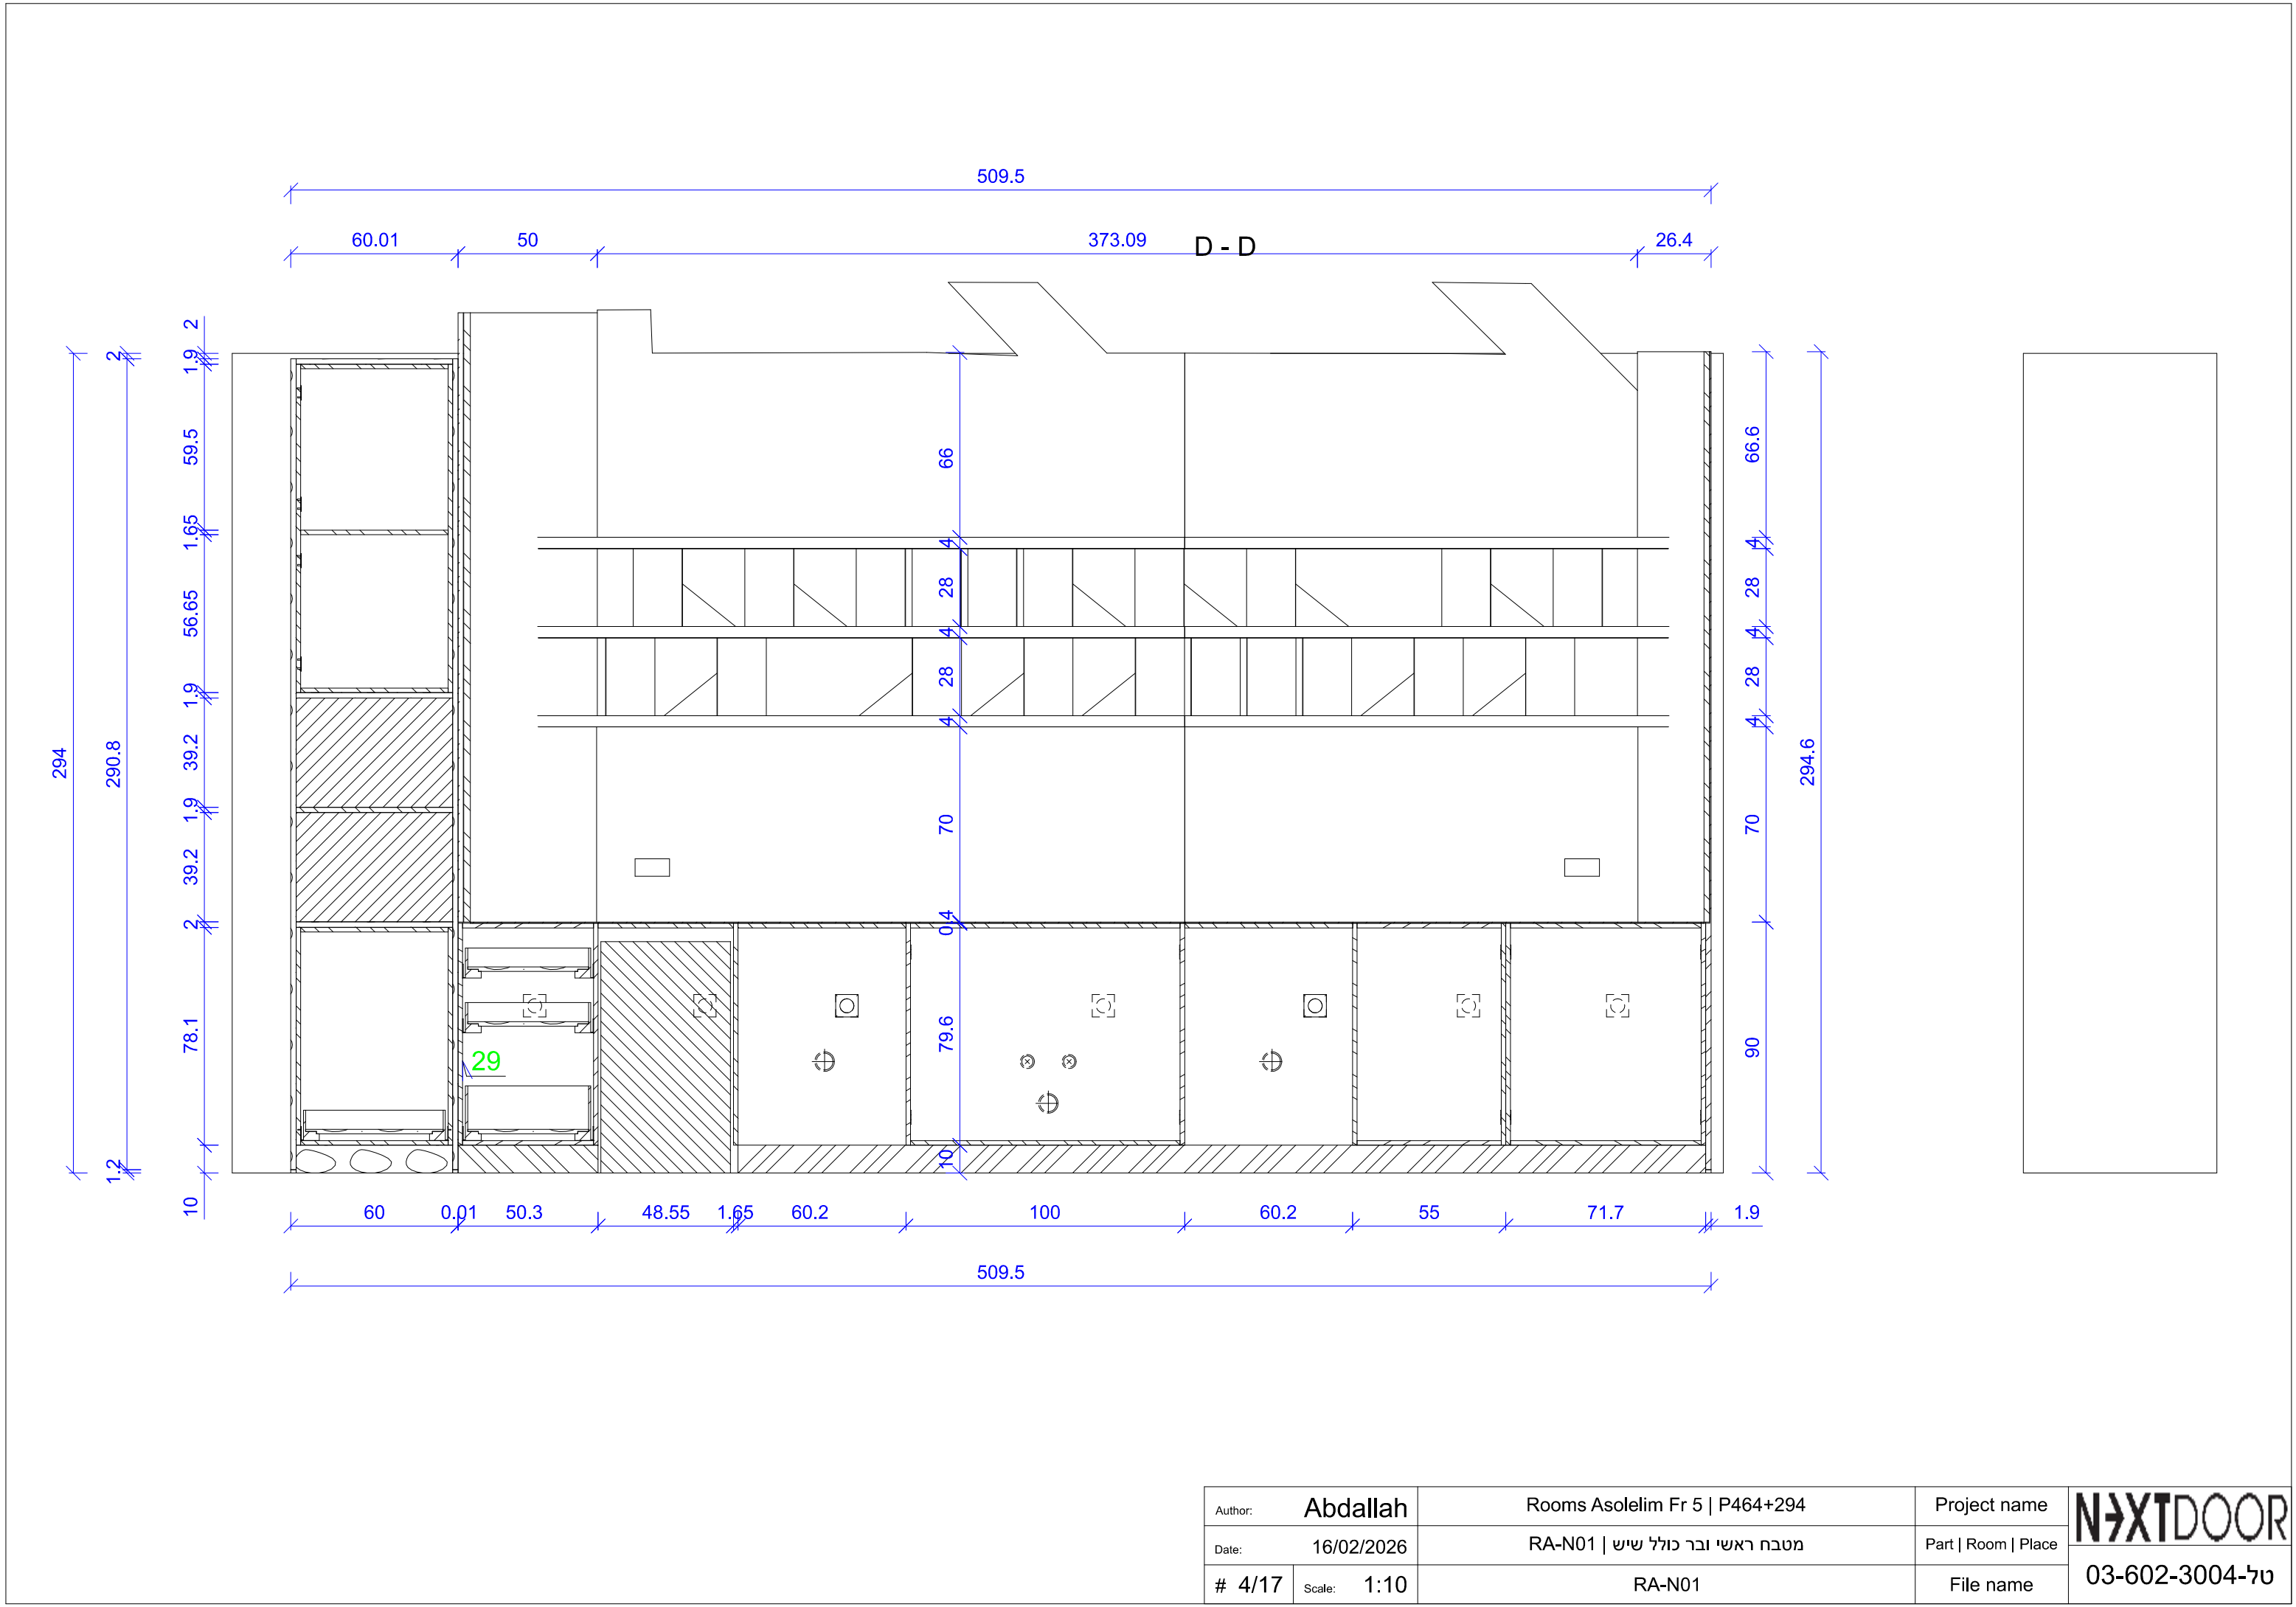


Author:	Abdallah	Rooms Asolelim Fr 5 P464+294	Project name	N→XTDOOR
Date:	16/02/2026	מטבח ראשי ובר כולל שיש RA-N01	Part Room Place	
# 4/17	Scale: 1:10	RA-N01	File name	
				טל-03-602-3004

Technical drawing of a building section showing a long, low structure with a flat roof and a series of vertical supports. The drawing includes dimensions: 1.8, 39.41, 74, 274.09, 58.3, 1.9, 70, and 449.5. The structure is divided into sections by vertical walls, and the roof is shown with a dashed line indicating its profile. The drawing is a black and white line drawing with blue dimension lines and text.

Author: Abdallah		Rooms Asolelim Fr 5 P464+294	Project name	N→XTDOOR
Date: 16/02/2026		RA-N01 מטבח ראשי ובר כולל שיש	Part Room Place	
# 5/17	Scale: 1:10	RA-N01	File name	

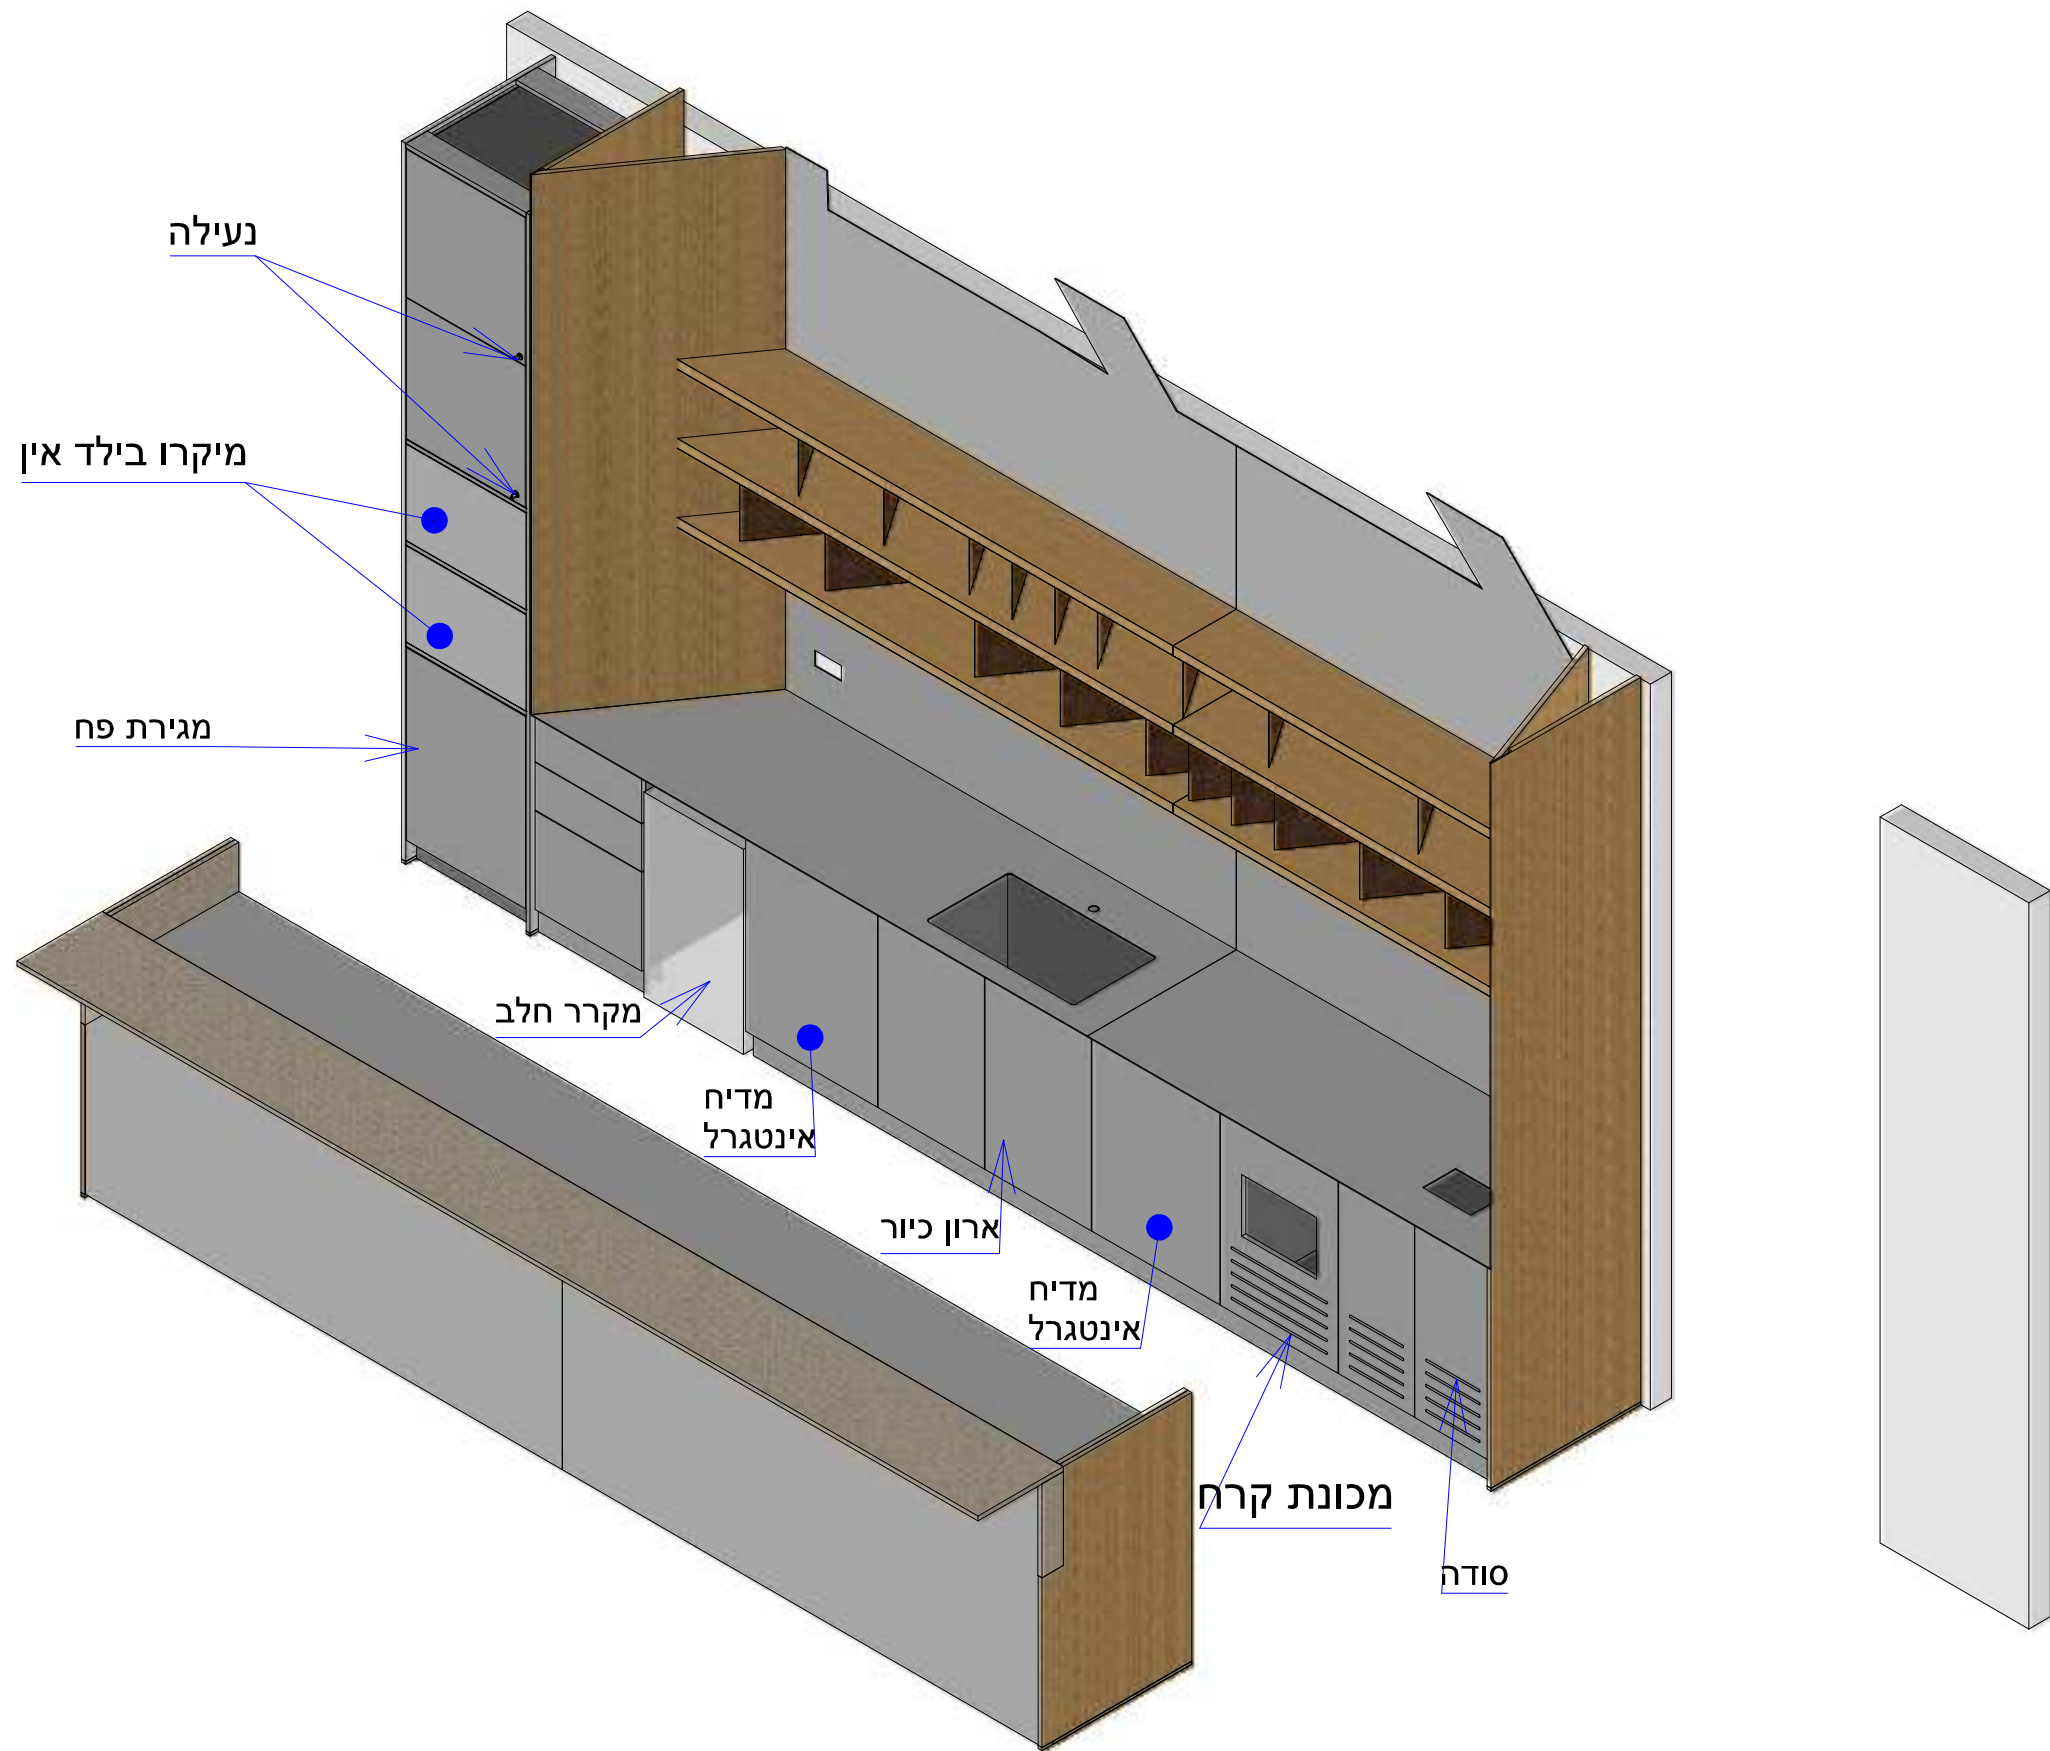

Author:	Abdallah	Rooms Asolelim Fr 5 P464+294	Project name	NXTDOOR טל-03-602-3004
Date:	16/02/2026	מטבח ראשי ובר כולל שיש RA-N01	Part Room Place	
# 8/17	Scale: 1:10	RA-N01	File name	

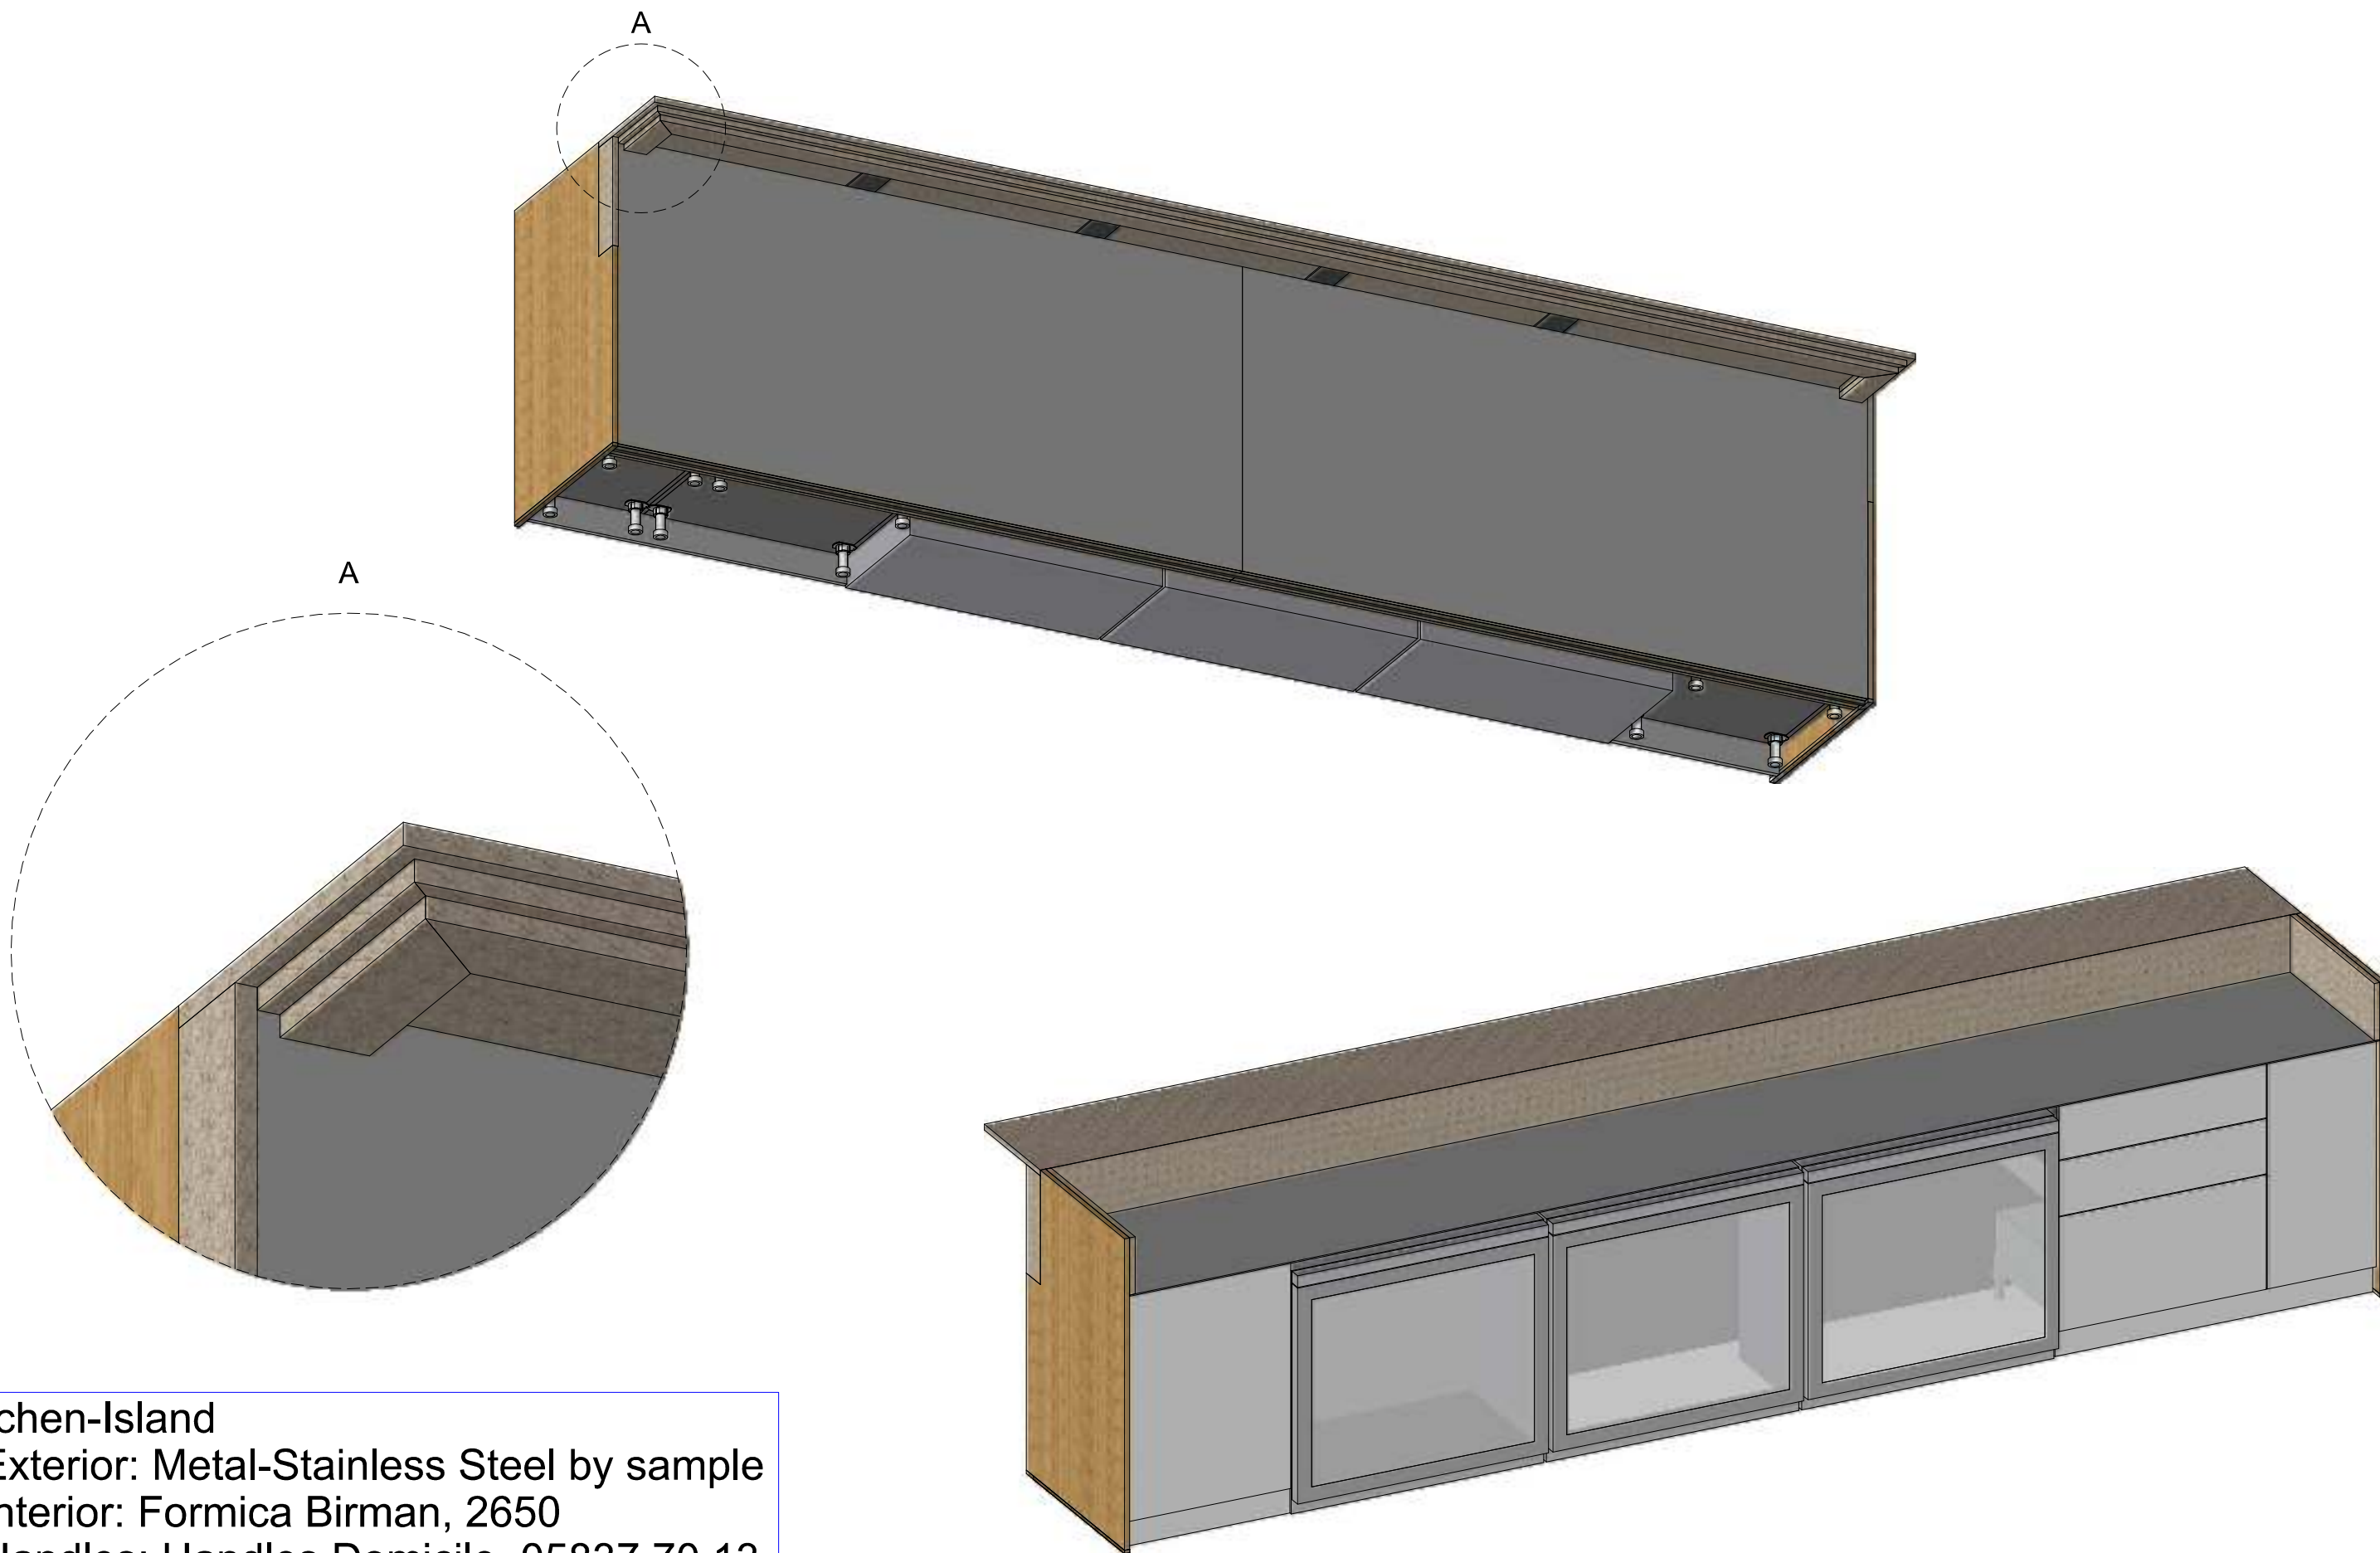

2: Kitchen-Island

2.1: Exterior: Metal-Stainless Steel by sample

2.2: Interior: Formica Birman, 2650


2.3: Handles: Handles Domicile, 05837.70.13

2.4: Toe kick: Metal-Stainless Steel by sample





2.5: Countertop: Stone Marble, Laba Rosa

2.6: Backsplash: Stone Marble, Laba Rosa

Author:	Abdallah	Rooms Asolelim Fr 5 P464+294	Project name	N→XTDOOR 03-602-3004-טל
Date:	16/02/2026	מטבח ראשי ובר כולל שיש RA-N01	Part Room Place	
#15/17	Scale: 1:10	RA-N01	File name	

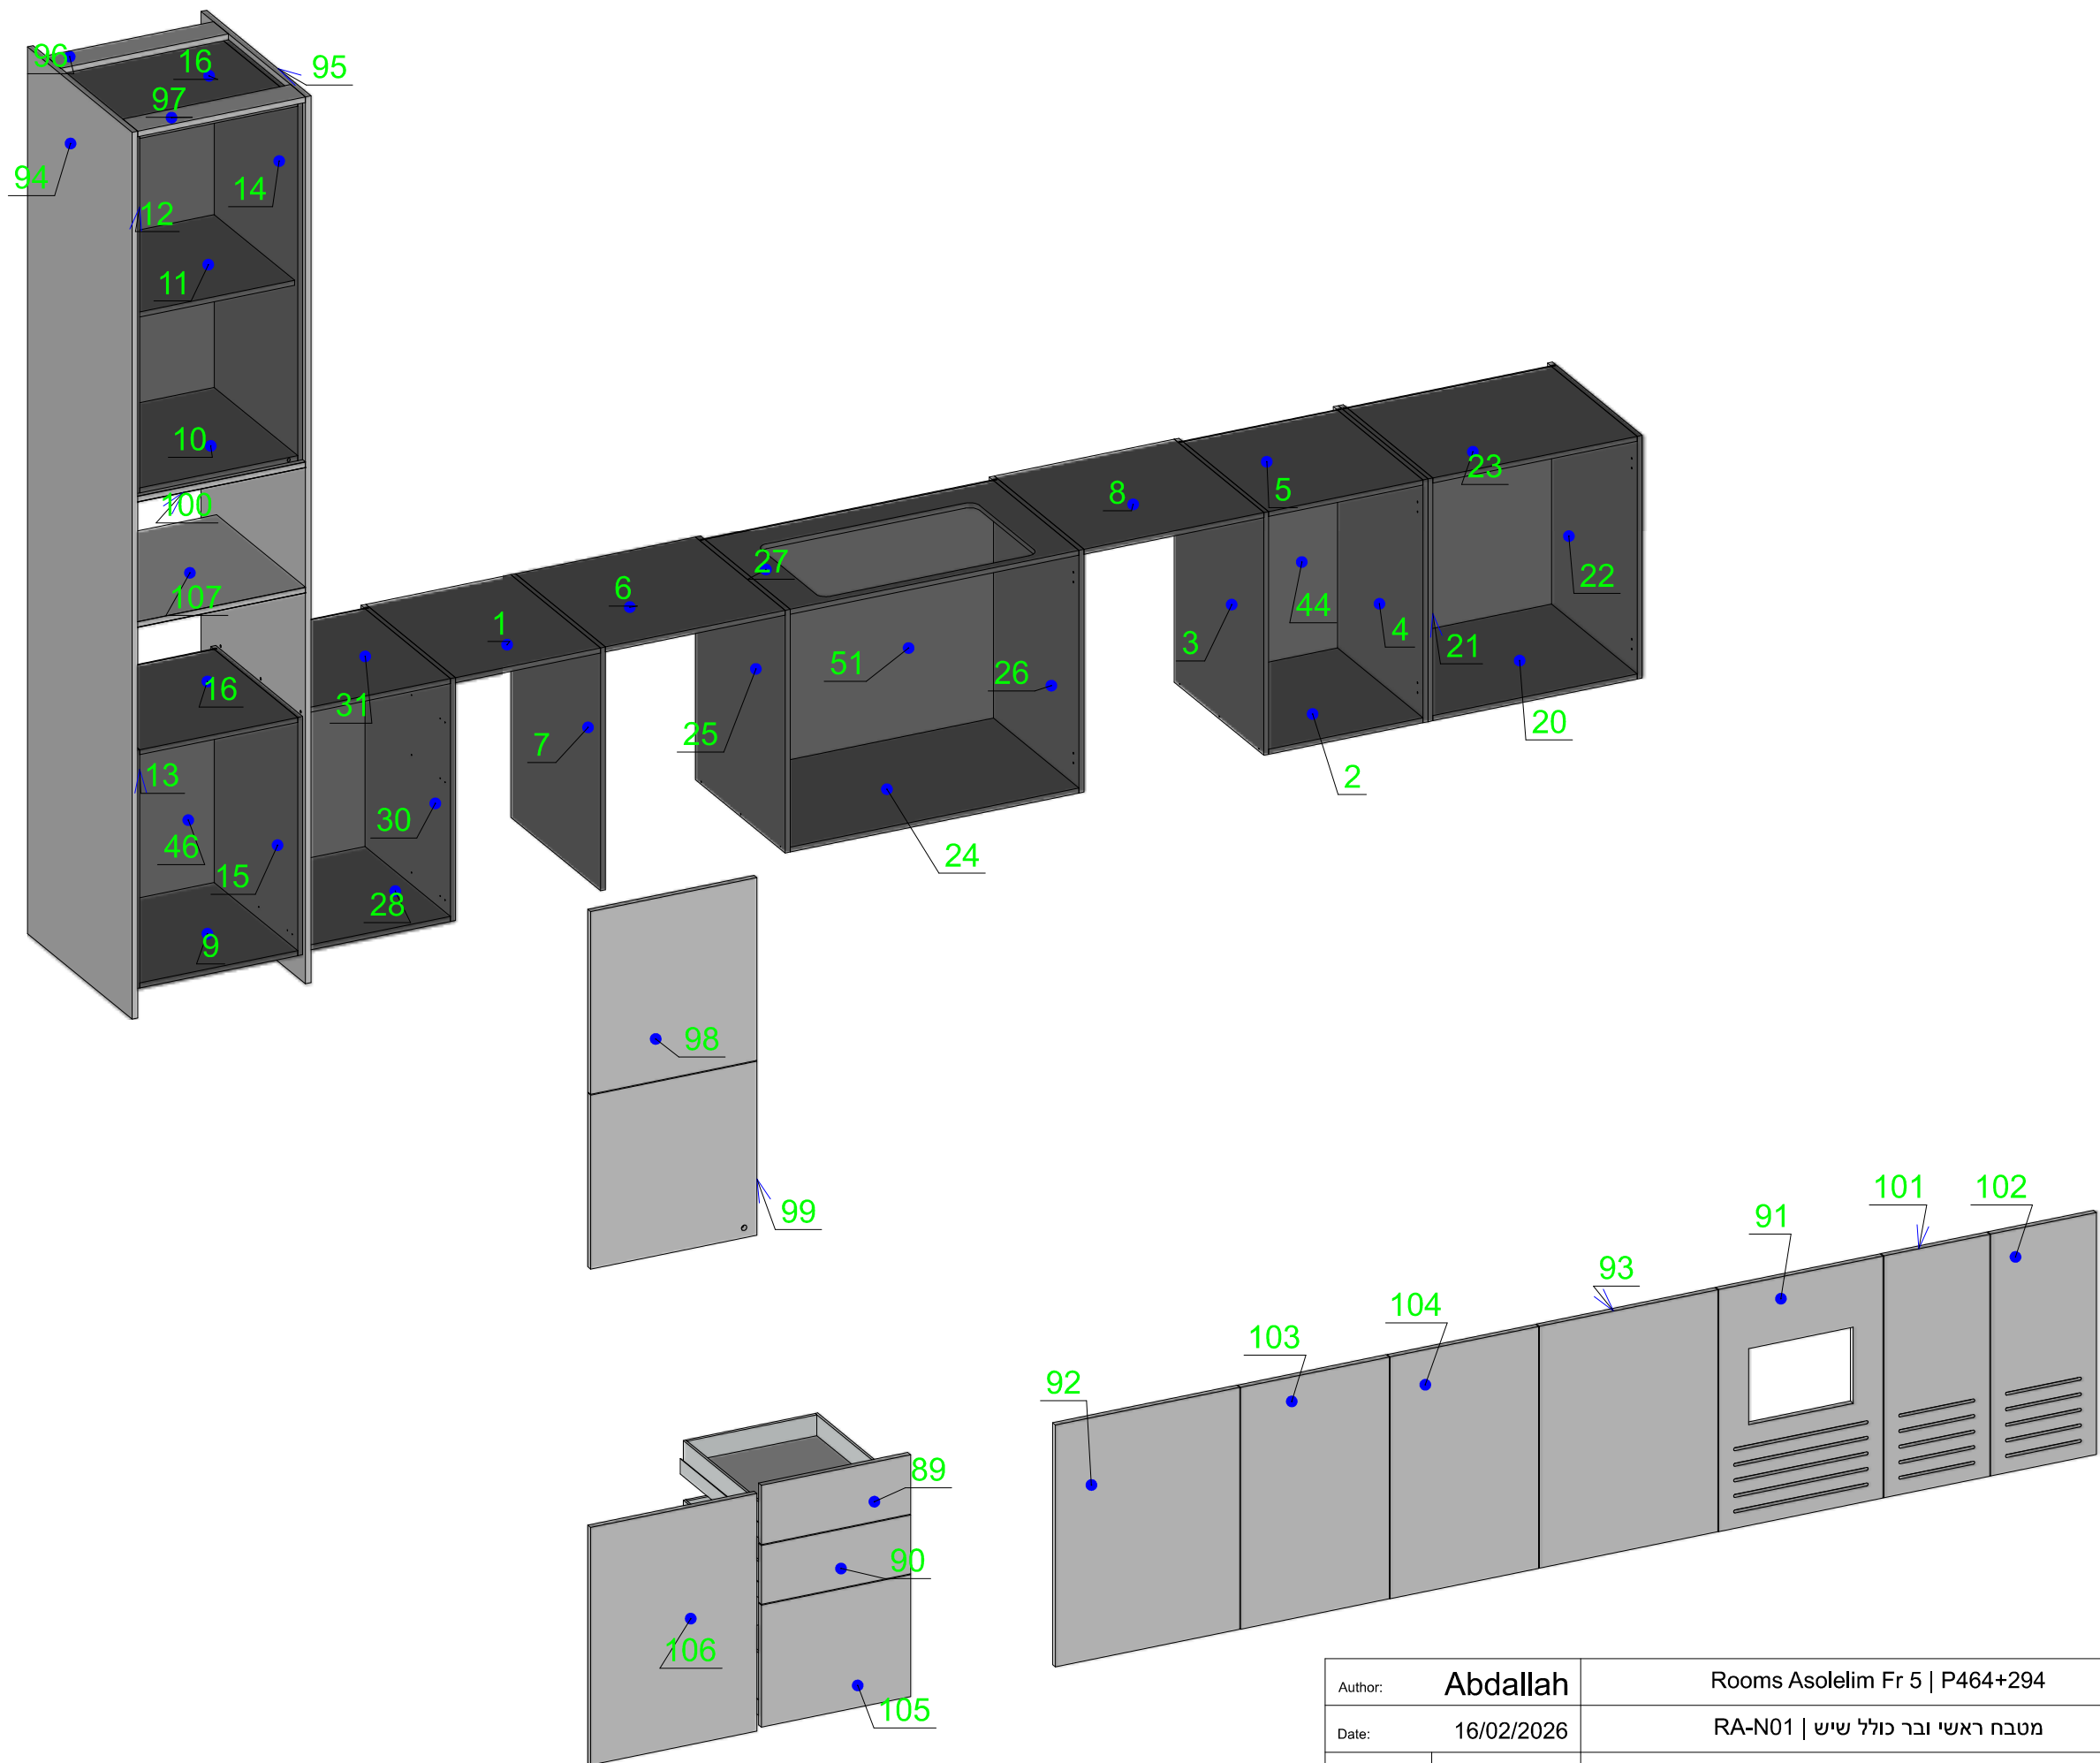

Author: Abdallah		Rooms Asolelim Fr 5 P464+294	Project name	NXTDOOR טל-03-602-3004
Date: 16/02/2026		מטבח ראשי ובר כולל שיש RA-N01	Part Room Place	
#16/17	Scale: 1:10	RA-N01	File name	

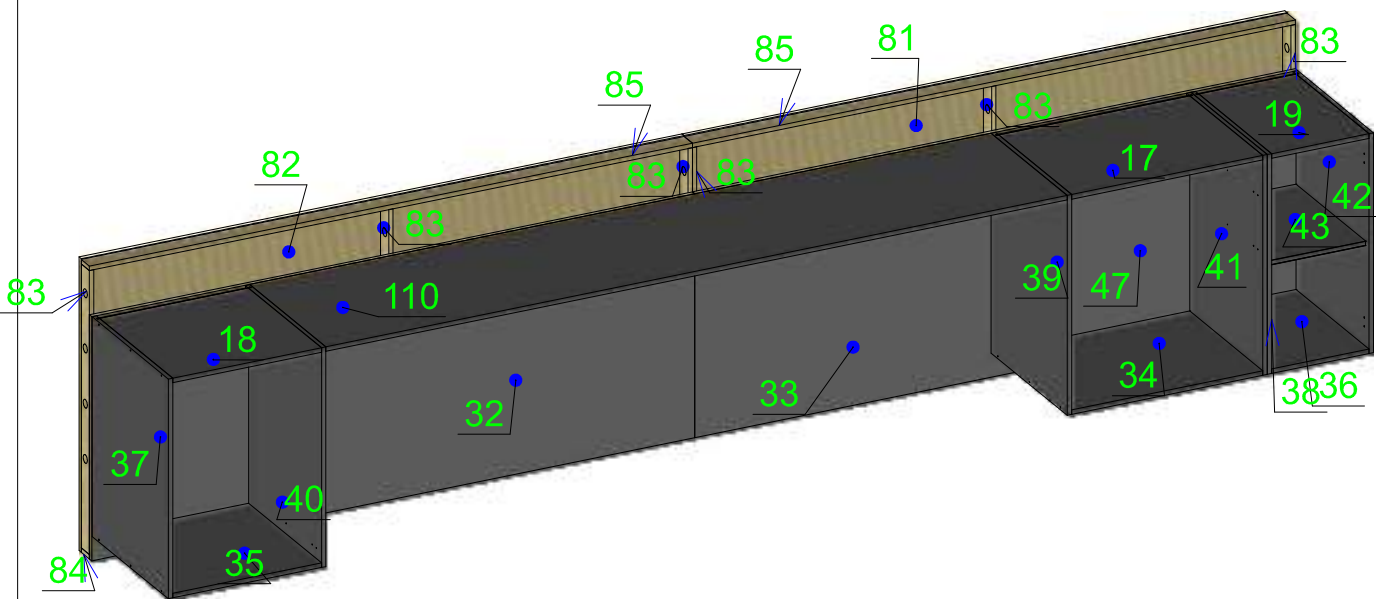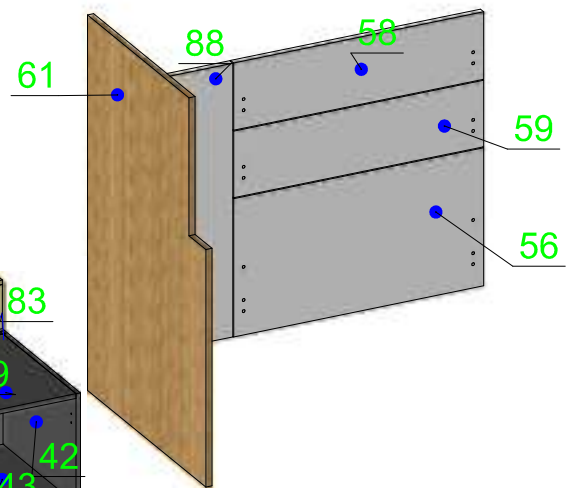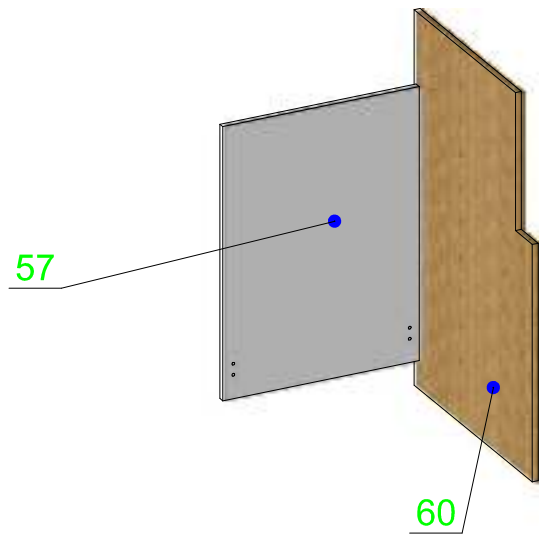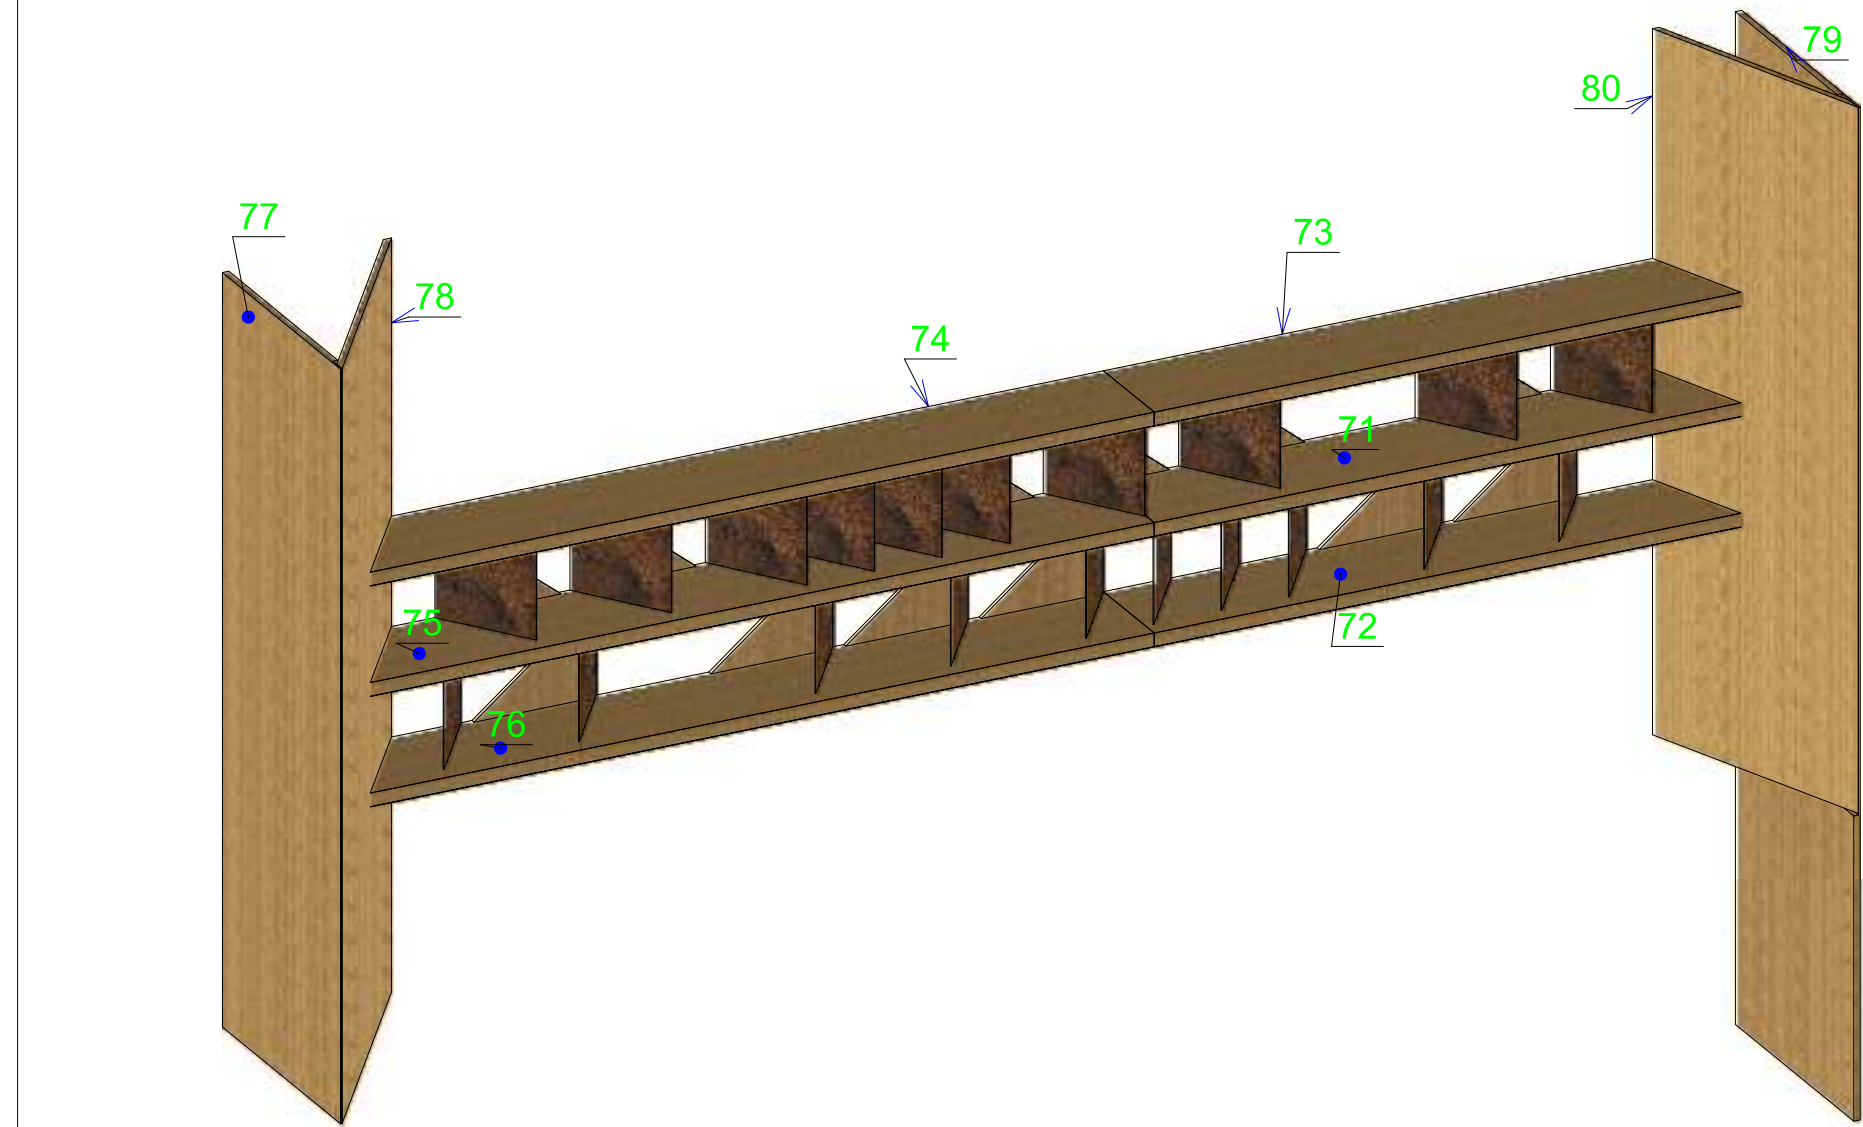

Author: Abdallah		Rooms Asolelim Fr 5 P464+294	Project name	N→XTDOOR 03-602-3004-טל
Date: 16/02/2026		מטבח ראשי ובר כולל שיש RA-N01	Part Room Place	
#17/17	Scale: 1:10	RA-N01	File name	